


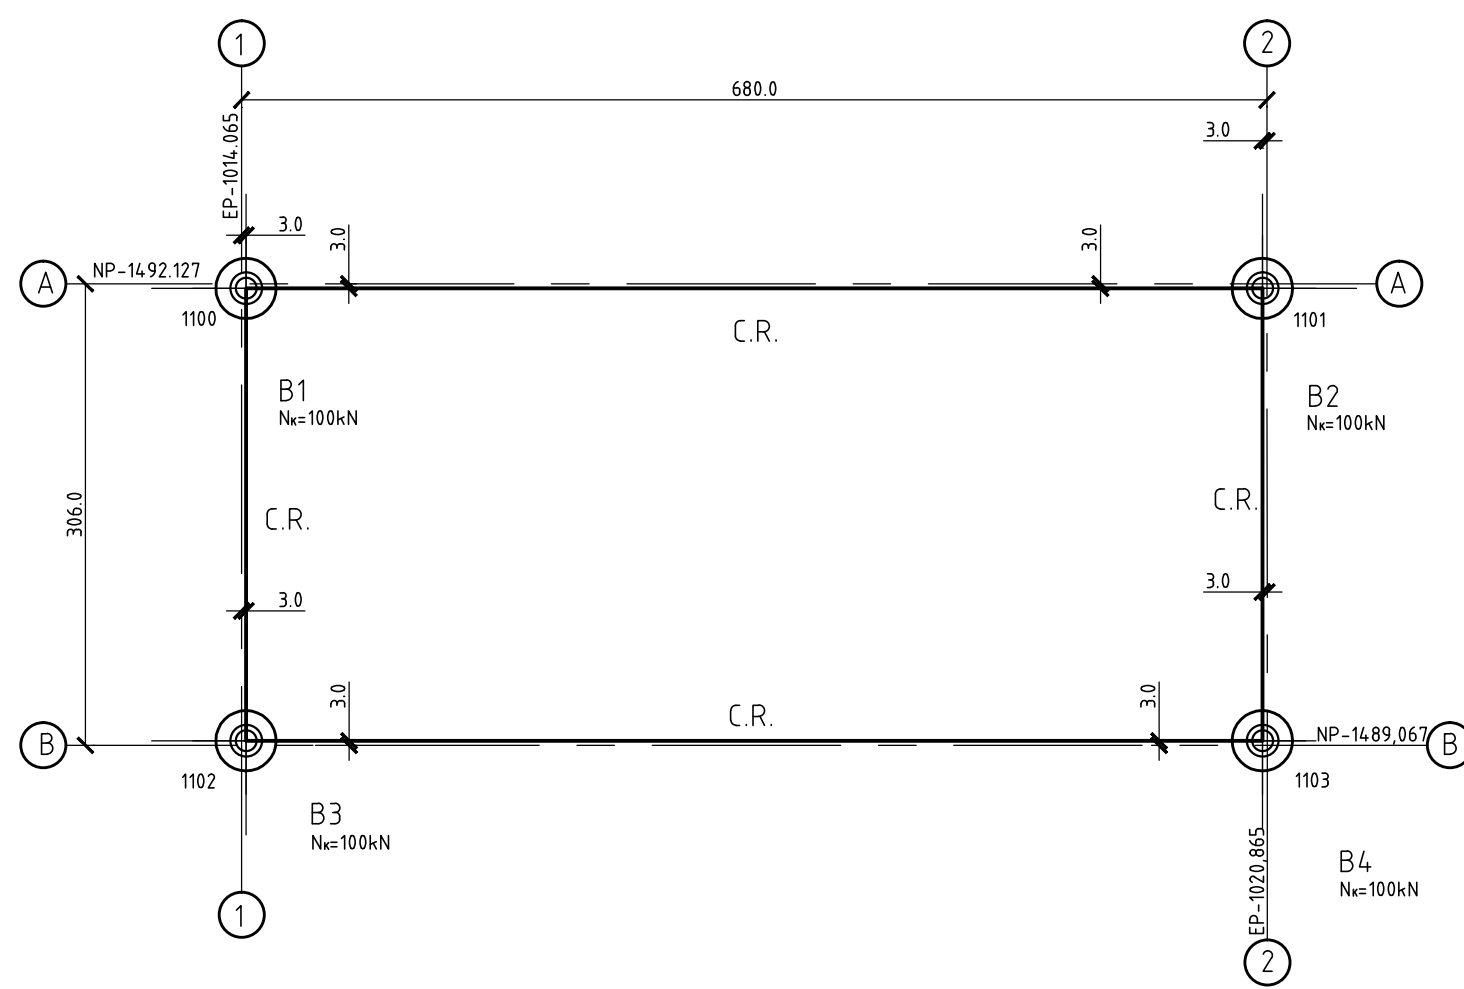



QUADRO DE ESTACAS PORTARIA II

APOIOS		ESTACAS			
NÚMERO	CARGA (tf)	QUANTIDADE E TIPO DE ESTACA	CARGA/ESTACA (tf) (*)	NÚMERO DA ESTACA	COMPRIMENTO DA ESTACA (m)
B1	10	1 #40cm	10,5	1100	10,0
B2	10	1 #40cm	10,5	1101	10,0
B3	10	1 #40cm	10,5	1102	10,0
B4	10	1 #40cm	10,5	1103	10,0

(*) - CARGAS CONSIDERANDO O PESO PRÓPRIO DAS FUNDAÇÕES.
(**) - COMPRIMENTO TOTAL DAS ESTACAS EM RELAÇÃO A COTA +5,50m.

OBS.: DEPENDENDO DOS RESULTADOS DA INVESTIGAÇÃO COMPLEMENTAR O COMPRIMENTO DAS ESTACAS PODERÁ SOFRER ALTERAÇÃO.

DETALHE ESPIRAL
SEM ESCALA

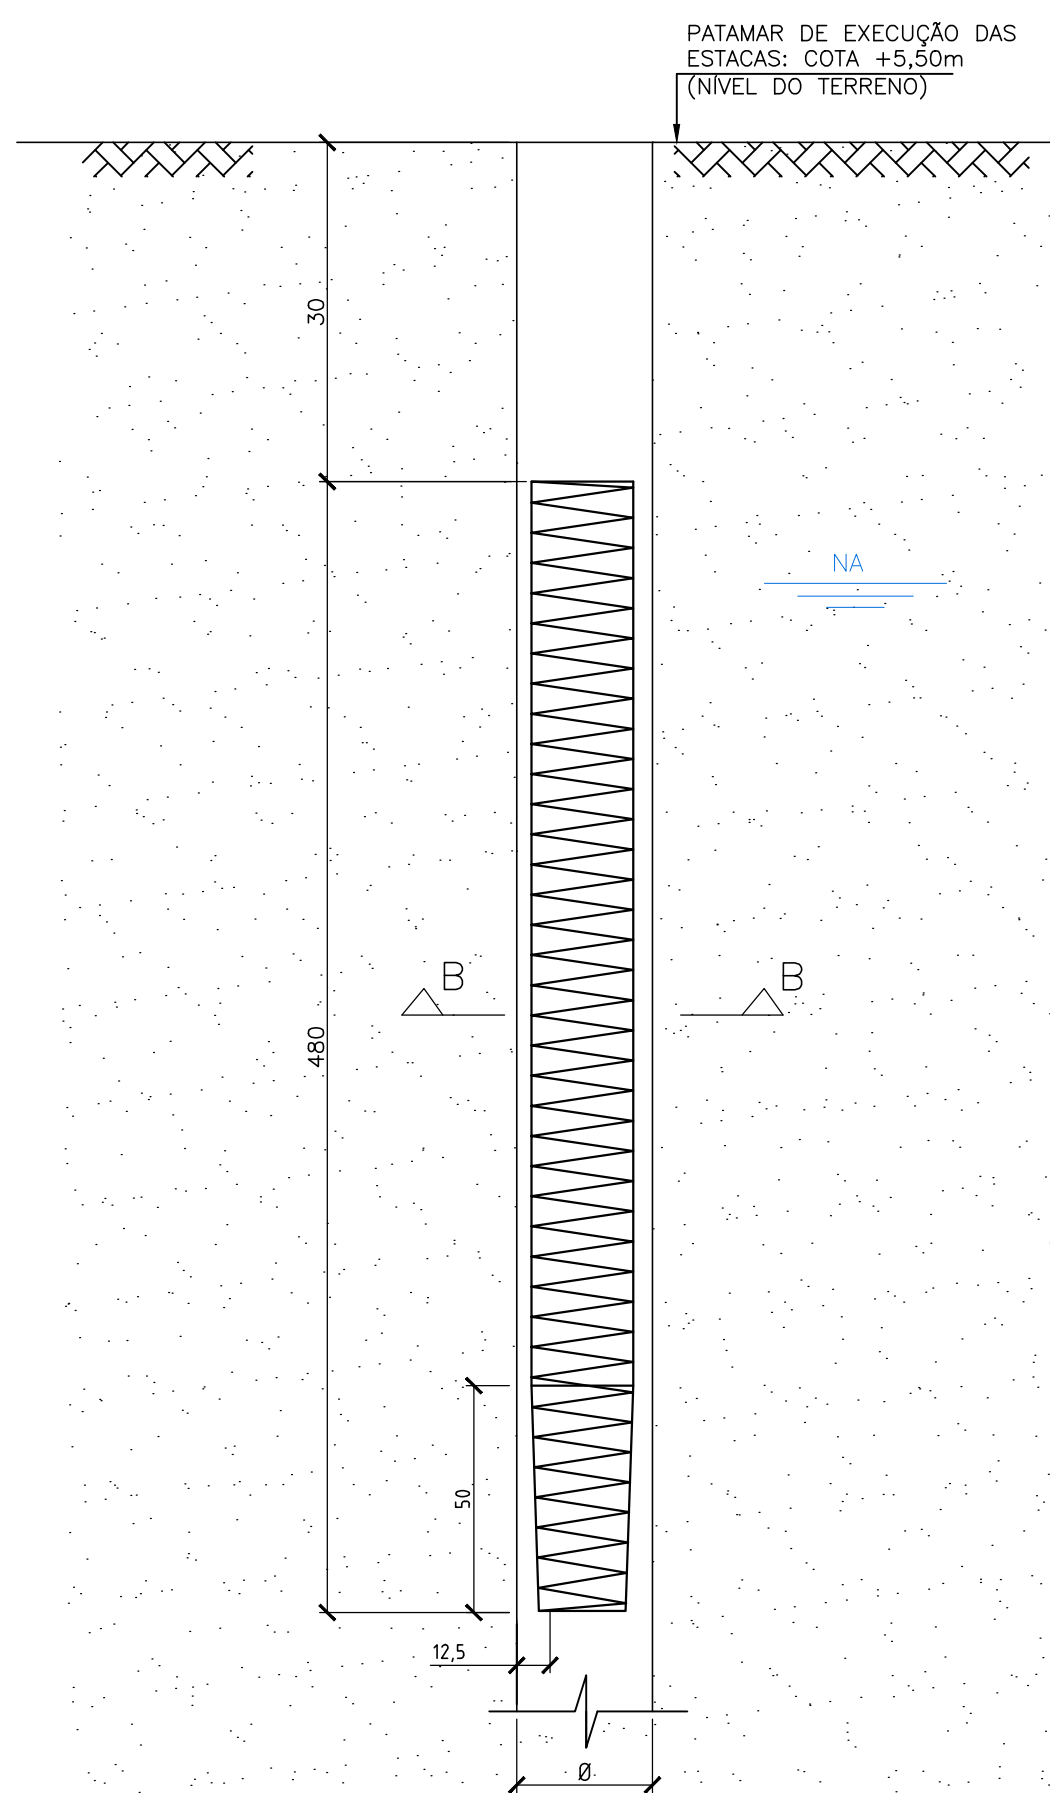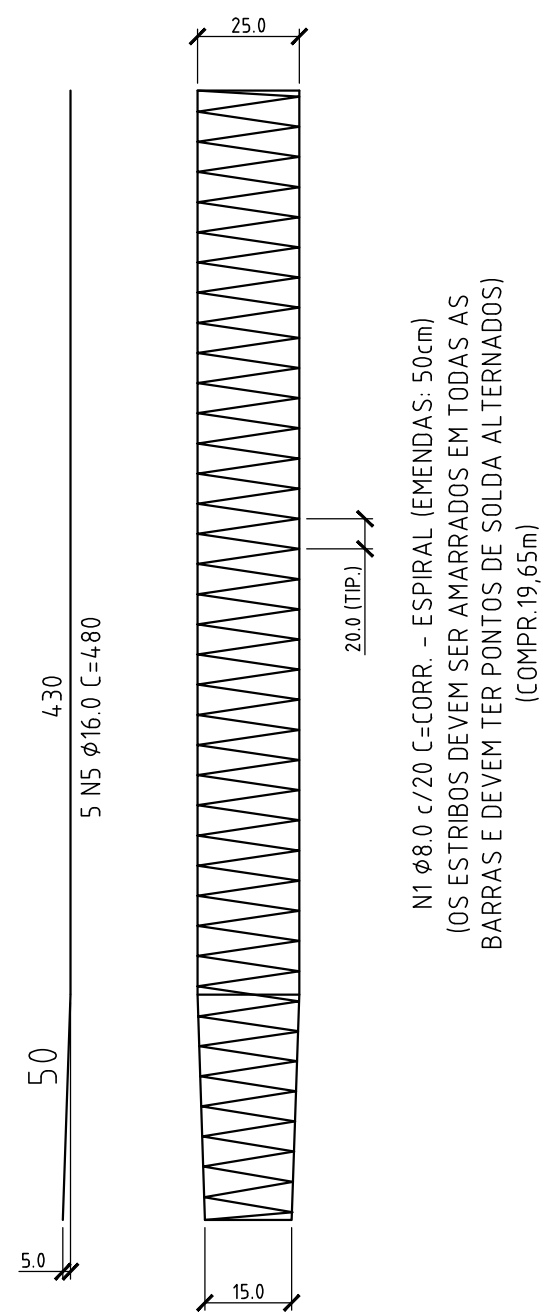


CONCRETO $f_{ck}=25$ MPa
AÇO CA-50 SOLDÁVEL.

DIÂMETRO DA ESTACA HÉLICE	ARMADURA LONGITUD. MÍNIMA	COMPRIMENTO ÚTIL DA ARMADURA	COMPRIMENTO TOTAL DA ARMADURA
Ø40 cm	5 Ø16,0mm	4,0m	4,8m

ESTRIBOS CIRCULARES DE AÇO CA-50:
ø8mm A CADA 20cm COM TRANSPASSE DE 35cm

OS ESTRIBOS SERÃO AMARRADOS EM TODAS AS BARRAS E SERÃO SOLDADOS.

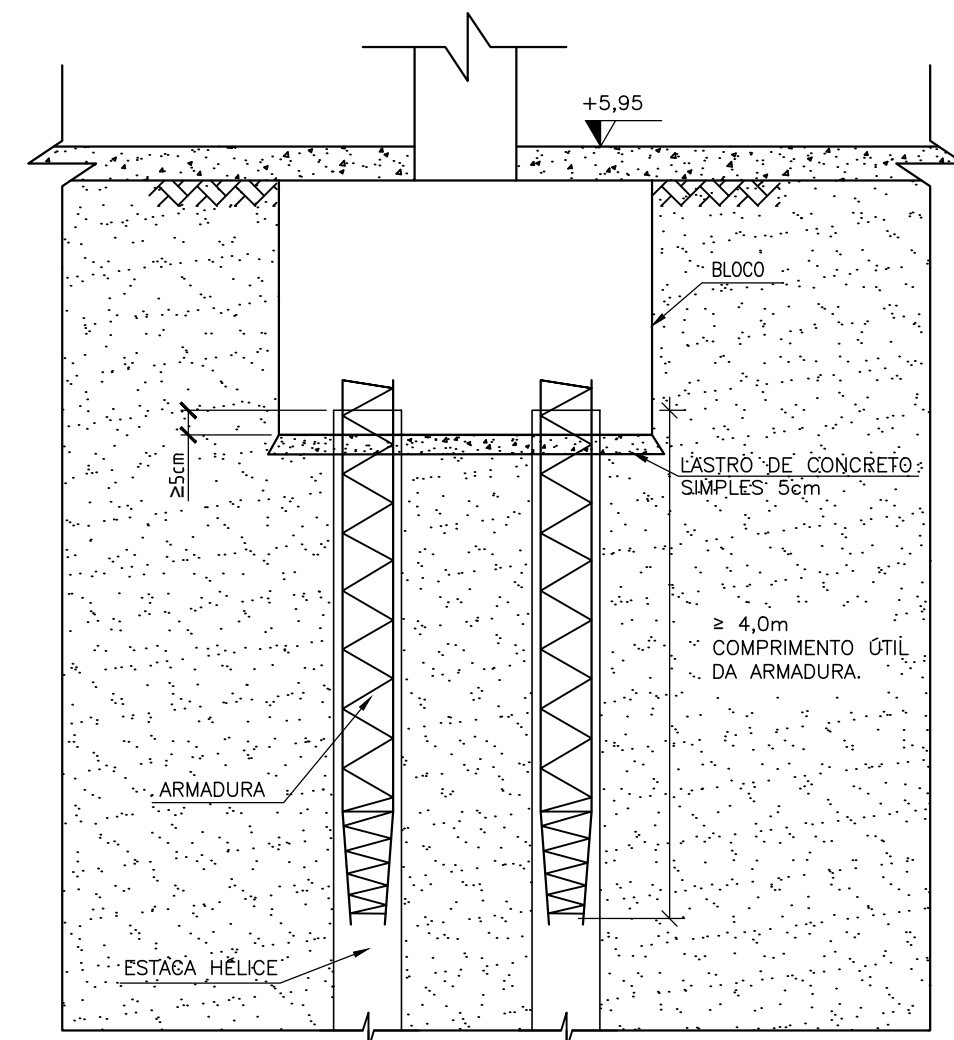

- P70069-000-DW-0051-001 - ARRANJO GERAL - PLANO DIRETOR - COORDENADAS E NÍVEIS DE IMPLANTAÇÃO
- P70069-406-DW-1711-121 - FORMAS

1) O PATAMAR DE EXECUÇÃO DAS ESTACAS SERÁ A COTA +5,50m. AS PROFUNDIDADES SÃO INDICADAS NO QUADRO DE ESTACAS. CASO A PERFORAÇÃO DE ESTACA NÃO CONSIGA Atingir o comprimento mínimo especificado, comunicar ao projetista de fundações. SONDAGENS ADICIONAIS PODERÃO SER SOLICITADAS.

2) SERÁ EXIGIDO UM ARRASAMENTO (CORTE DO TOPO DA ESTACA) MÍNIMO DE 50cm PARA EXECUÇÃO DOS BLOCOS DE COROAMENTO (VER DETALHE 1).

3) AS ESTACAS ESTÃO LOCADAS EM RELAÇÃO AOS RESPECTIVOS PONTOS DE CARGA, CUJA LOCAÇÃO É DE RESPONSABILIDADE DO PROJ. ESTRUTURAL.

4) O CENTRO DE GRAVIDADE DE CADA GRUPO DE ESTACAS DEVE COINCIDIR COM O CENTRO DE CARGA DO RESPECTIVO PILAR

51 O DIMENSIONAMENTO ESTRUTURAL DOS BLOCOS SOBRE ESTACAS DEVE AGUARDAR O TÉRMINO DO ESTACAMENTO PARA SE LEVAR EM CONTA POSSÍVEIS EXCENTRICIDADES DE EXECUÇÃO. OS LEVANTAMENTOS DAS EXCENTRICIDADES DE EXECUÇÃO DEVERÃO SER ENVIADOS À GEOCONSULT PARA ANÁLISE.

6) O CONTROLE TECNOLÓGICO DO CONCRETO E DO AÇO DAS ESTACAS DEVE SEGUIR AS ORIENTAÇÕES DO ITEM 7 DAS ESPECIFICAÇÕES DO ESTACAMENTO E AOS REQUISITOS DA ABNT.

7) O DESEMPENHO DAS FUNDAÇÕES DEVERÁ SER COMPROVADO MEDIANTE REALIZAÇÃO DE PROVA DE CARGA ESTATICA OU ENSAIOS DE CARREGAMENTO DINÂMICO CONFORME VIGORA A NBR6122/2010.

8) EM FUNÇÃO DOS RECALQUES E DA INTERAÇÃO SOLO-ESTRUTURA PODERÁ OCORRER REDISTRIBUIÇÃO DE CARGAS ENTRE OS PILARES, RESULTANDO EM VARIAÇÕES NOS VALORES DOS ESFORÇOS APRESENTADOS NA PLANILHA ORIGINAL DO PROJETO ESTRUTURAL. ASSIM, IMPORTANTE QUE O PROJETISTA ESTRUTURAL EXAMINE ESSES ASPECTOS E PROCEDA AOS AJUSTES QUE JULGAR NECESSÁRIOS. NO CASO OCORREREM MODIFICAÇÕES SIGNIFICATIVAS, ENVIÁ-LAS PARA O PROJETISTA DE FUNDAÇÕES PROCEDER, SE FOR O CASO, AS MODIFICAÇÕES NECESSÁRIAS.

9) NA ESCAVAÇÃO PARA EXECUÇÃO DE BLOCO DE COROAMENTO SOBRE AS ESTACAS COM O AUXÍLIO DE MÁQUINAS (RETROESCAVADEIRA OU SIMILAR), DEVE-SE OBSERVAR:

a) AS CAÇAMBAS (CONCHAS) DOS EQUIPAMENTOS DEVEM TER LARGURA INFERIOR A 50% DO ESPAÇAMENTO DISPONÍVEL ENTRE ESTACAS DO BLOCO A SER ESCAVADO;

10) DIMENSÕES EM CENTÍMETROS E ELEVAÇÕES EM METROS.

11) ESTE PROJETO OBEDECE EM GERAL A NBR 6122/2010 - PROJETO E EXECUÇÃO DE FUNDAÇÕES DA ABNT, A QUAL DEVE SER SEGUIDA NOS CASOS OMISSOS. DEVERÁ SER OBEDECIDO AINDA, NAQUILO QUE NÃO CONFLITAR COM A NORMA, O MANUAL DE ESPECIFICAÇÃO DE PRODUTOS E PROCEDIMENTOS DA ABEP PARA ESTACAS TIPO HÉLICE CONTÍNUA MONITORADAS.

QUADRO RESUMO DO ESTAQUEAMENTO

ESTACA	QUANTIDADE	TOTAL ESTIMADO (m)	ESTRIBO (kg)	ARMADURA LONGITUDINAL (kg)
Ø40cm	4	40,0	32,0	160,0


N° DA ESTACA

CONVENÇÕES:

- ESTACA HÉLICE CONTÍNUA Ø40cm
CARGA DE TRAB. À COMPRESSÃO: 40tf

— C.R. - CINTA DE RIGIDEZ

PLANTA-CHAVE

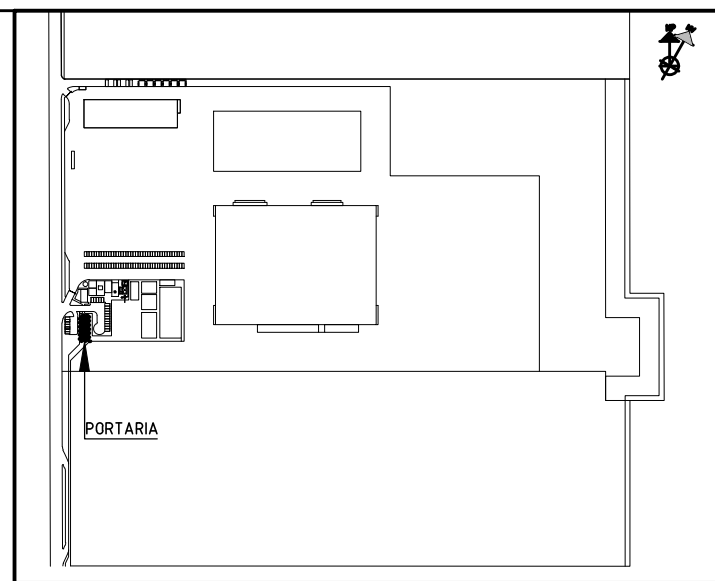

1	EPC	ACRESCENTADAS COORDENADAS DOS EIXOS B-2		13/12/2012	MSANCHES	CLY CUNHA	NPENIEIROL
0	EPA	EMITIDO PARA APROVAÇÃO		28/11/2012	GEOCONSULT	CLY CUNHA	NPENIEIROL
REV	PROPOSTO	MODIFICAÇÃO		DATA	DESENHO	VERIFICADO	APROVADO
PROPOSTO DE EMISSÃO							
ASB-AS-BUILT		CAN-CANCELADO	ECC-CONFORME COMPRADO	EPI-EMIÇÃO FINAL	EPC-PARA CONSTRUÇÃO	EPCO-PARA COTAÇÃO	
EPCO-PARA DE TALHAMENTO		EPA-PARA APROVAÇÃO		EPI-PARA INFORMAÇÃO		ECC-PARA COMISSÃO/CONTA	
CANCELAR E SUBSTITUIR O DESENHO NÚMERO:		LIBERADO ☐	LIBERADO C/ RESALVAS ☐	ESTE DESENHO É DE PROPRIEDADE DA FLEXIBRÁS, E NÃO PODE SER COPIADO.			
CANCELADO E SUBSTITUÍDO PELO DESENHO NÚMERO:		NÃO LIBERADO ☐	VISTO ☐	REPRODUZIDO SEM SUBMETIDO A TERCEIROS SEM A SUA AUTORIZAÇÃO POR ESCRITO.			
ÓRGÃO		ASS.	DATA				
ESTA LIBERACÃO NÃO ISENTA A CONTRATADA DE SUAS RESPONSABILIDADES CONTRATUAIS							

APROVAÇÃO		DATA	TÍTULO ÁREA 406-PORTARIAS PORTARIA 2 LOC. E ARMADURA DAS ESTACAS P70069 - NOVA FÁBRICA - BUILDING	
DESENHADO	RENAN	28/11/12		
VERIFICADO	TAYRO	28/11/12		
APROVADO	UBERESCLAS	28/11/12		
 			MATERIAL: _____ ESCALA: IND. _____ PESO (kg): _____ REFERENCIA: _____ NUMERO: P70069-406-DW-1430-002 _____ REVISAO: 1 _____	

LINHAS - CINZA - 9 = 0,20 / COR 253
LINHAS DE PISO / LAYOUT - ROSA - 11 = 0,10 / COR PRETO
LINHAS A DEVOIR - LARANJA - 30 = 0,30 / COR 30
LINHAS DE VEGETAÇÃO - VERDE - 104 = 0,20 / COR 104
LINHAS A CONSTRUIR - LILÁS - 191 = 0,20 / COR 1
LINHAS - VERMELHO - 10 = 0,15 / COR 10
LINHAS - AMARELO - 40 = 0,15 / COR 40
LINHAS - AZUL - 50 = 0,15 / COR 50

5 LINHAS:
LINHAS DE COTAS - VERMELHO - 1 = 0,15 / COR PRETO
LINHAS DE CORTES - AMARELO - 2 = 0,50 / COR PRETO
LINHAS - VERDE - 3 = 0,15 / COR PRETO
LINHAS DE ESQUADRIA / TEXTOS - CYAN - 4 = 0,20 / COR PRETO
LINHAS DE LIMITE - AZUL - 5 = 0,30 / COR PRETO
LINHAS TRACELADAS - MAGENTA - 6 = 0,25 / COR PRETO
LINHAS DE CONTORNOS / FORMATO - PRETO - 7 = 0,4 / COR PRETO

ESPECIAL CIVIL
ARQUITETURA