


CORTE A-A
ESC.1:75

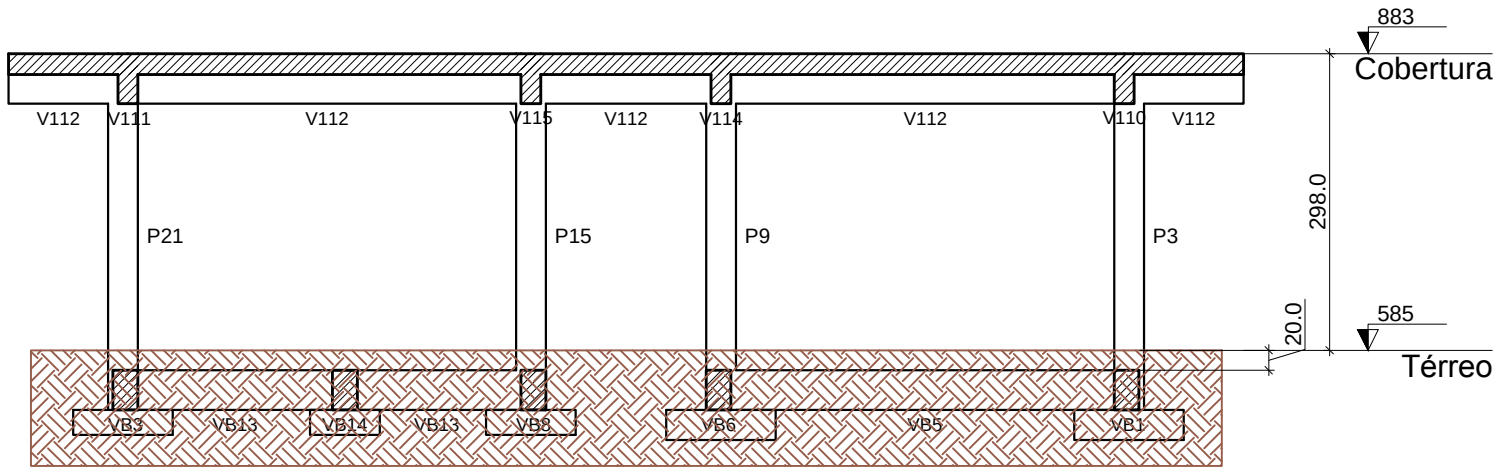

CORTE B-B
ESC.1:75

NOTAS

ESPECIFICAÇÕES DOS MATERIAIS:

1. CONCRETO: SAPATAS, VIGAS BALDRAMES E PILARES EM CONCRETO CLASSE C30 QUE NAS CONDIÇÕES DE UTILIZAÇÃO DEVE APRESENTAR, PARA CLASSE DE AGRESSIVIDADE AMBIENTAL IV (NBR 6119:2007):
 - f_{ck} = 30 MPa (300 kg/cm²) ou maior
 - CONSUMO MÍNIMO DE CIMENTO: 350 kg/m³
 - FATOR ÁGUA/CIMENTO = 0,45 (ou menor)
 - MASSA ESPECÍFICA APARENTE = 2400 kg/m³ (ou menor)
 - MÓDULO DE ELASTICIDADE SECANTE = 28,7 GPa (ou maior) PARA TENSÃO APLICADA DE 30 MPa AOS 28 DIAS DE IDADE
 - DIÂMETRO MÁX. DO AGREGADO GRAUÍDO = 19mm (Brita 1)

CURA

1. PREVER UM PERÍODO DE CURA ÚMIDA POR NO MÍNIMO 7 DIAS

ACO

1. RESISTÊNCIAS:
 - CADA f_{yk} = 500MPa
 - CADA f_{yk} = 600MPa
2. COBRIMENTO DA ARMADURA:
 - 5,0 cm SAPATAS
 - 4,5 cm VIGAS E PILARES

OBS.: OS COBRIMENTOS QUE NÃO OBEDECEREM ESSA ESPECIFICAÇÃO ESTÃO INDICADOS NOS DESENHOS DE ARMADURAS.

EXIGÊNCIAS DE DURABILIDADE:

1. CLASSE DE AGRESSIVIDADE AMBIENTAL: IV;
 2. AGRESSIVIDADE: MUITO FORTE;
 3. CLASSIFICAÇÃO GERAL DO TIPO DE AMBIENTE PARA EFEITO DE PROJETO: RESPINGOS DE MARE;
 4. RISCO DE DETERIORAÇÃO DA ESTRUTURA: ELEVADO
- CONCRETO DE CIMENTO PORTLAND PREPARADO, CONTROLE E RECEBIMENTO PROCEDIMENTO

NORMAS NBR 12655 - SET2006

ESTA NORMA É APLICÁVEL A CONCRETO DE CIMENTO PORTLAND PARA ESTRUTURAS MOLDADAS NA OBRA, ESTRUTURAS PRÉ-MOLDADAS E COMPONENTES ESTRUTURAIS PRÉ-FABRICADOS PARA EDIFICAÇÕES E ESTRUTURAS DE ENGENHARIA. O CONCRETO PODE SER MISTURADO NA OBRA, PRÉ-MISTURADO OU PRODUZIDO EM USINA DE PRÉ-MOLDADOS. ESTA NORMA SE APLICA A CONCRETOS NORMAIS, PESADOS OU LEVES.

UNIDADE DAS DIMENSÕES


- 1- NÍVEIS, CORTES E DIMENSÕES EM CENTÍMETROS.
- 2- AS ELEVACÕES INDICADAS REFEREM-SE AO ZERO DNM. EL. DNM = EL. IBGE + 0,836 m.
- 3- COORDENADAS PLANAS UTM DATUM SAD 69.

DESENHOS DE REFERÊNCIA

ACU-3.DES-2.3100-15-EGS-013-R00

LEGENDA

PLANTA CHAVE

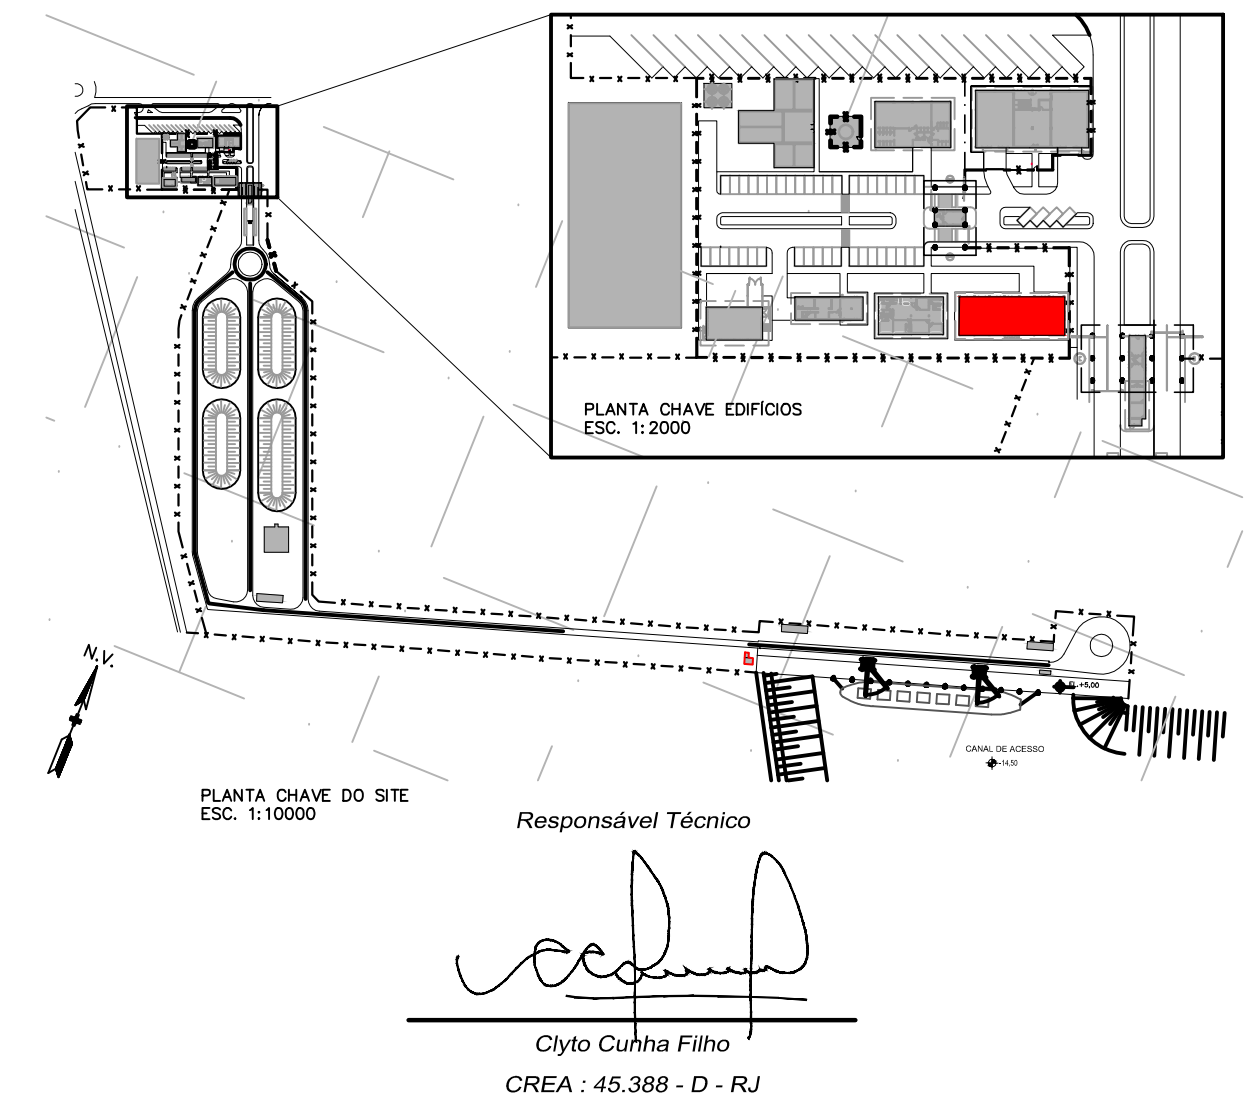

A	25/03/15	E	EGS	ATENDIDO COMENTÁRIOS CONFORME GRD 106-15 - PARA CONSTRUÇÃO
O	20/01/15	B	EGS	EMISSION PARA COMENTÁRIOS
REV.	DATA	TIPO	POR	DESCRIÇÃO DAS REVISÕES

EMISSIONS

TIPO DE EMISSION	(A) PRELIMINAR (B) P/COMENTÁRIOS (C) P/CONHECIMENTO	(D) P/COTAÇÃO (E) P/CONSTRUÇÃO (F) CONFORME COMPRADO	(G) CONFORME CONSTRUÍDO (H) CANCELADO (I) APROVADO	(J) LIB. P/COMPRA (M) CERTIFICADO
------------------	---	--	--	--------------------------------------

PRUMO LOGÍSTICA GLOBAL		AQU OPERAÇÕES PORTUARIAS S/A		
engesique		PORTO DO AQU - PROJETO EXECUTIVO INSTALAÇÕES ONSHORE - CIVIL T2 - TERMINAL DE MÚLTIPLO USO - TMULT - FASE I 04-EDIFÍCIO ADMINISTRATIVO CORTES		
RESPONSÁVEL	DATA	ESCALA	No. PRL: AQU-3.DES-2.3100-11-EGS-060	REV. A
PROJ. ENG.ALEXANDRE	16/01/15	INDICADA	No. PROJETISTA:	FORMATO A1
DES. WANDERSON	19/01/15			
VERIF. ENG.REINALDO	20/01/15			
APROV. ENG.CLYTO	20/01/15			