



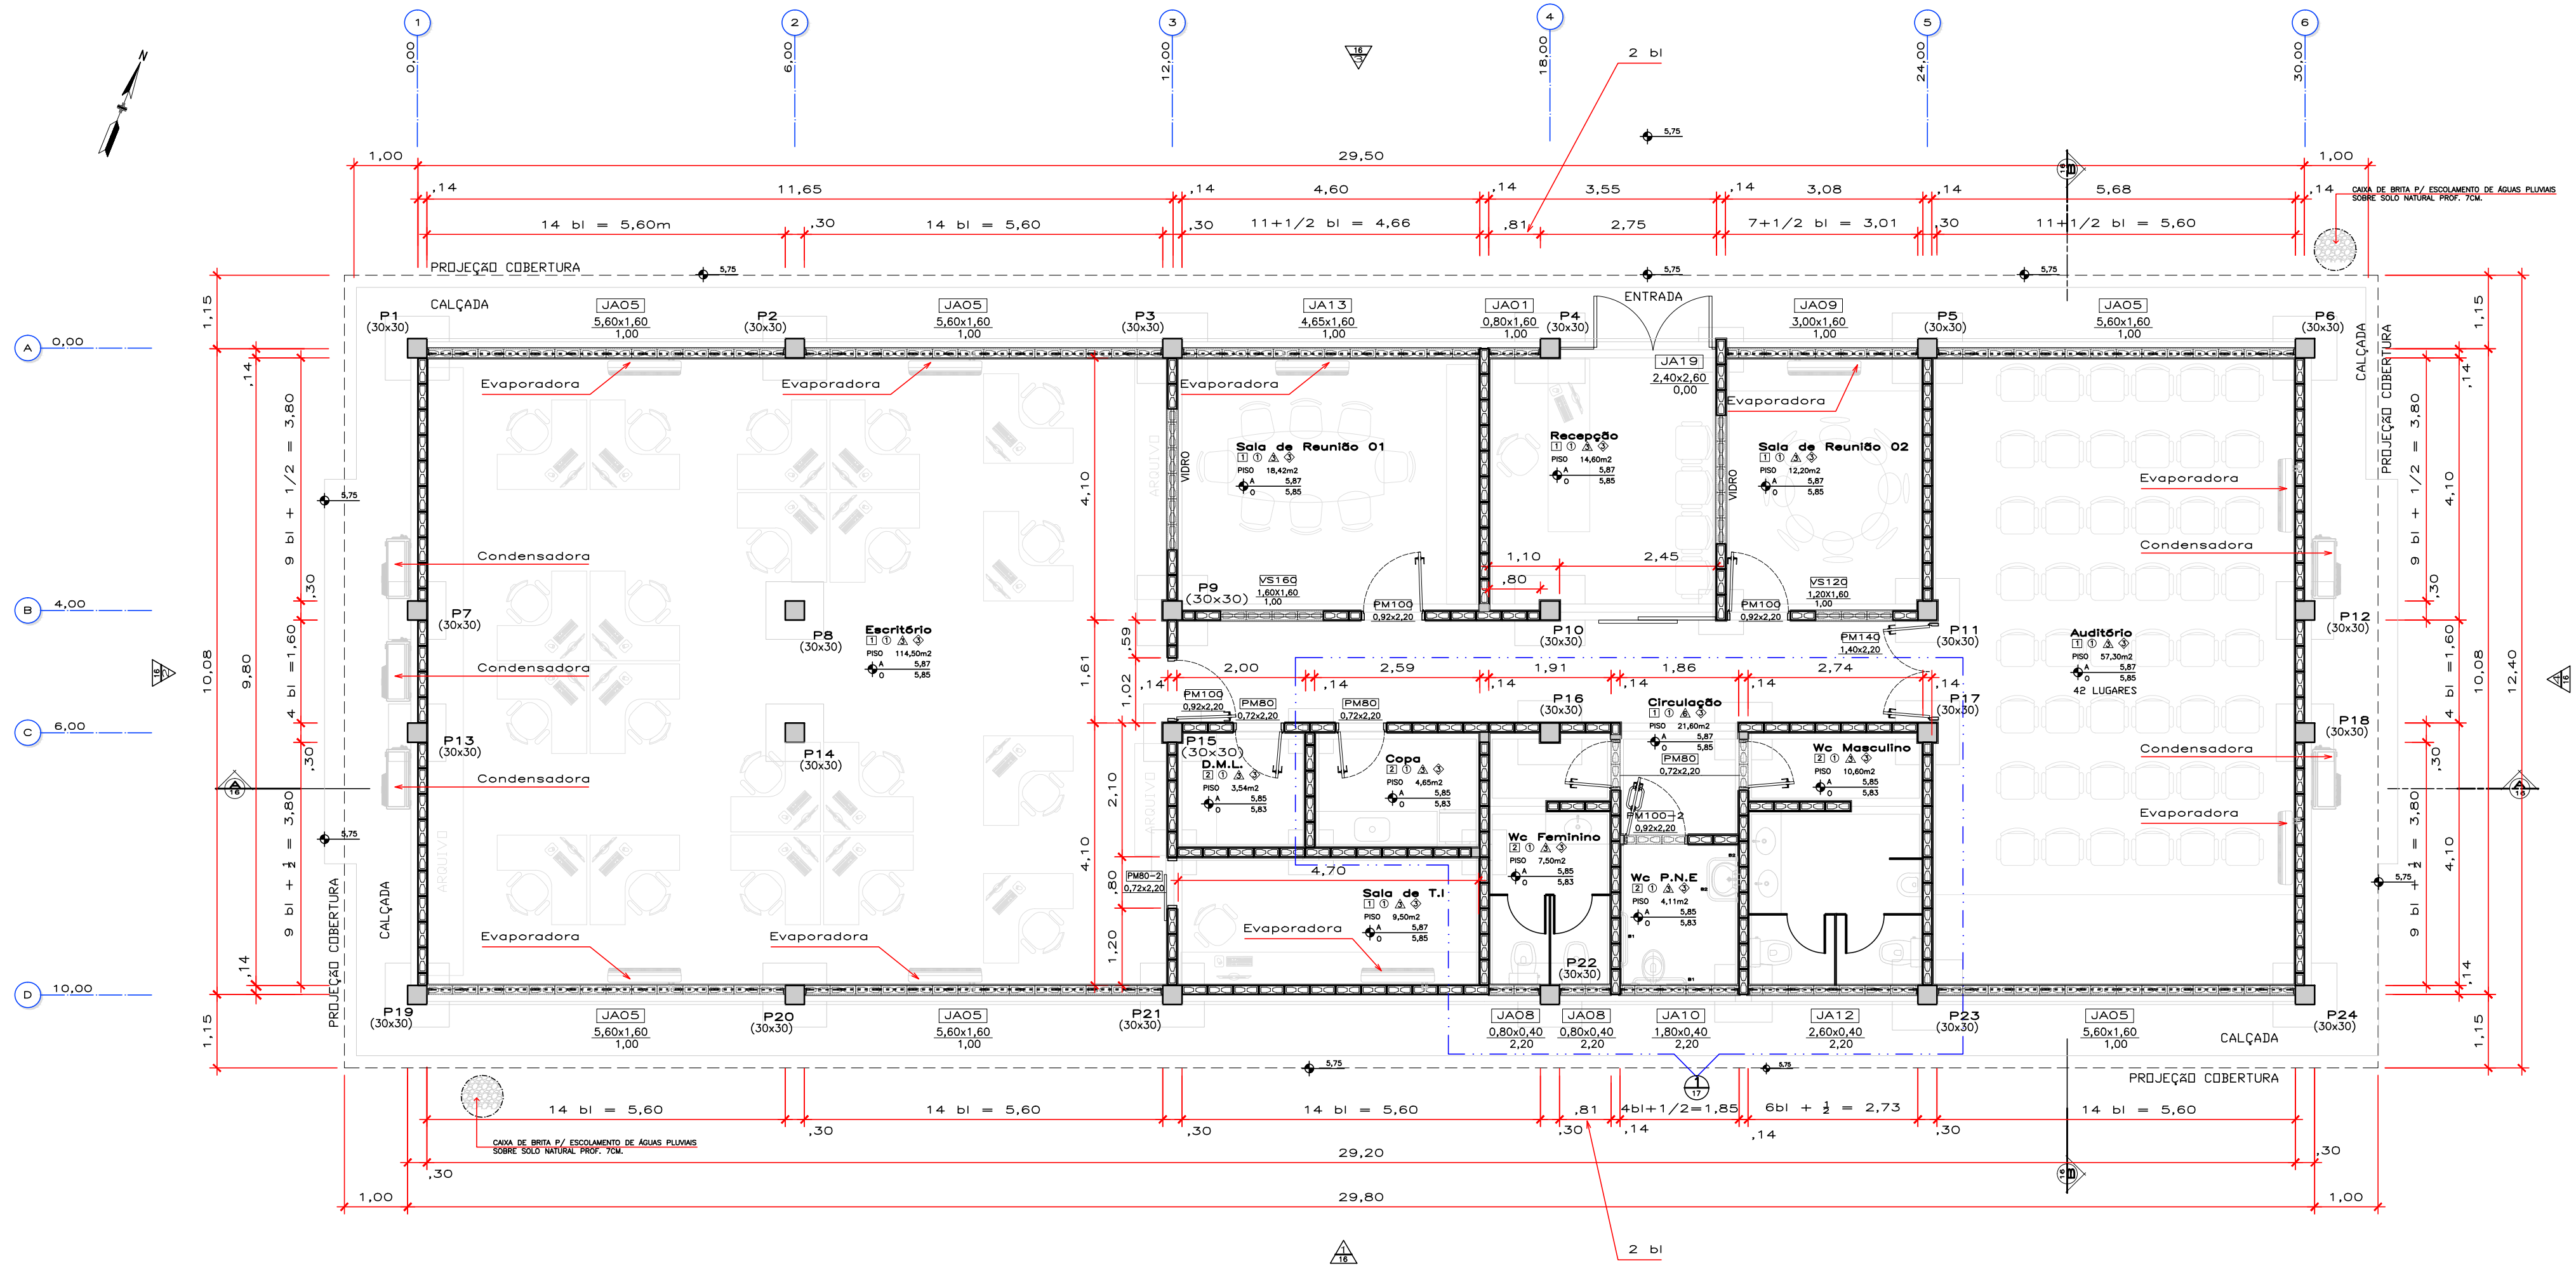

04 EDIFÍCIO ADMINISTRATIVO
TÉRREO
C: 1/2000
E: 1/2000

ÁREA TOTAL CONSTRUÍDA:
298,40m²
ÁREA TOTAL OCUPADA:
380,60m²

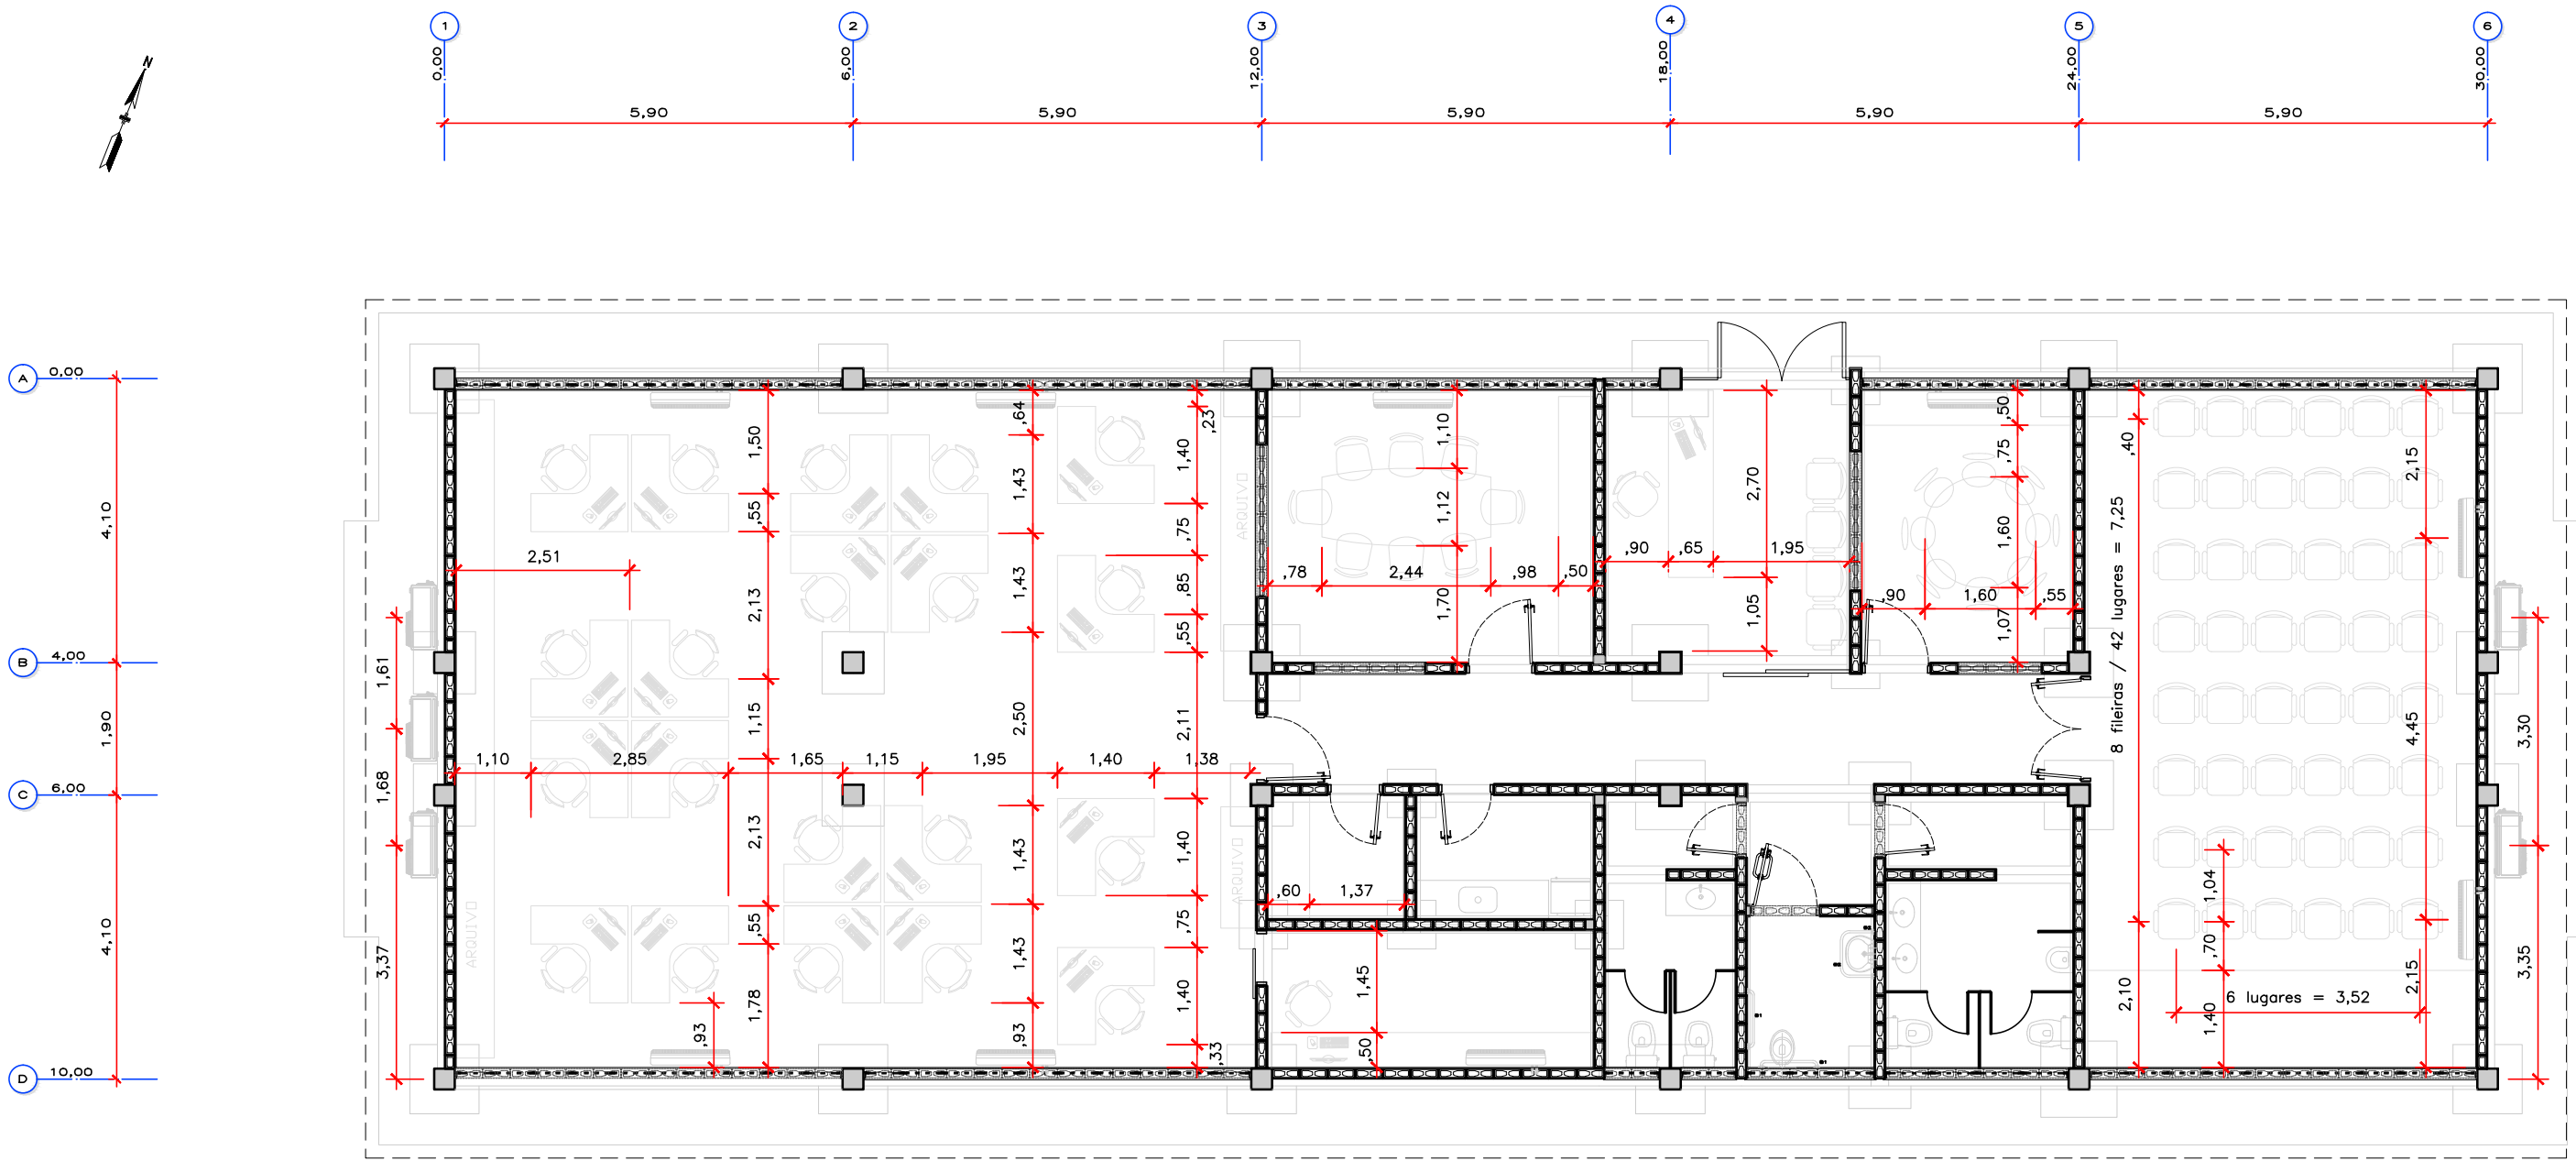

04 EDIFÍCIO ADMINISTRATIVO
TÉRREO
C: 1/2000
E: 1/2000

NOTAS

- 1- NÍVEIS, COORDENADAS E DIMENSÕES EM METRO.
- 2- AS ELEVÇÕES INDICADAS REFEREM-SE AO ZERO DHN.
EL. DHN = EL. IBGE + 0,836 m.
- 3- COORDENADAS PLANAS UTM DATUM SAD 69.
- 4- VER TABELA DE ESQUADRIAS NA FOLHA: AÇU-3.DES-2.3100-15-EGS-089
- 5 - O SISTEMA DE AR CONDICIONADO PREVISTO SERÁ O SPLIT SYSTEM

DESENHOS DE REFERÊNCIA


Projeto básico do prédio administrativo. Folhas: AÇU-2.DES-2.3100-15-RAM-209 rev.B
AÇU-2.DES-2.3100-15-RAM-210 rev.B
AÇU-2.DES-2.3100-15-RAM-210 rev.B
Implantação: AÇU-3.DES-2.3100-14-EGS-001 rev.0

LEGENDA

LEGENDA DE ACABAMENTOS

REVESTIMENTO PISO	
1	KORODUR - PISO DE ALTA RESISTÊNCIA, POLIDO, COR BEGE, COM JUNTAS METÁLICAS
2	CERÂMICA ELIANE - MOD. CARO PLUS GRAY 45x45 DE ALTO TRÁFEGO P1-5 - ASSENTADO COM CIMENTO COLANTE ACIII CINZA - REJUNTE COM JUNTA 3mm COR PINUS FAS. ELIANE.
3	PISO CIMENTADO LISO NO TRAJO 1:3 DE CIMENTO E AREIA.
4	CANCELADO
5	CONTRAPISO DE CONCRETO POLIDO, CONF. PROJ. DE ESTRUTURA
REVESTIMENTO RODAPÉ	
1	CANCELADO
2	MESMO MATERIAL APLICADO NA PAREDE
3	RODAPÉ (H=10CM) EM GRANITO CINZA ANDORINHA.
4	RODAPÉ (H=10CM) FAIXA DE CIMENTADO
REVESTIMENTO PAREDE	
1	PINTURA PVA COR BEGE SOBRE BLOCOS DE CONCRETO APARENTE.
2	PINTURA PVA BRANCA SOBRE ARGAMASSA.
3	RODAPÉ (H=10CM) EM GRANITO CINZA ANDORINHA, SEGUIDO DE CERÂMICA ELIANE SLIM BRANCO 30x40CM, C/ JUNTAS 2mm COR BRANCO NEVE, ASSENTADO COM ARGAMASSA COLANTE ACIII CINZA, ATE ALTURA DE 1,80m. SEGUIDO DE RODA-MEIO (H=10CM) EM GRANITO CINZA ANDORINHA E ACIMA DISTO PINTURA PVA BRANCA SOBRE ARGAMASSA.
4	CERÂMICA ELIANE, MOD. DIAMANTA BRANCO BRILHO,32,5x59, RETIFICADA, JUNTA 1mm C/ REJUNTE BRANCO EPOXI, ATE O TETO
5	DIVISÓRIAS DE H=2,00m TOTAL, INSTALADA A 0,20m DO PISO. GRANITO CINZA ANDORINHA.
6	DIVISÓRIAS COM REVESTIMENTO EM LAMINADO MELAMINICO NAS DUAS FACES.
7	PINTURA COM VERNIZ POLIURETANO INCORLOR
REVESTIMENTO TETO	
1	PINTURA EM TINTA PVA NA COR BRANCO NEVE SOBRE LAJE REBOCADA E EMBOÇO DESEMPENADO.
2	PINTURA EM TINTA PVA NA COR BRANCO NEVE SOBRE MASSA PVA SOBRE FORRO EM GESSO COMUM, REMOVÍVEL
3	COBERTURA EM ESTRUTURA ESPACIAL DE ALUMÍNIO ANODIZADO NATURAL COM EMPENA EM CHAPA CORRUGADA DE ALUMÍNIO ANODIZADO PRETO
4	FORRO DE LAMBRÉ DE PVC BRANCO REMOVÍVEL LAVAVEL REGUA 10cm.

PLANTA CHAVE

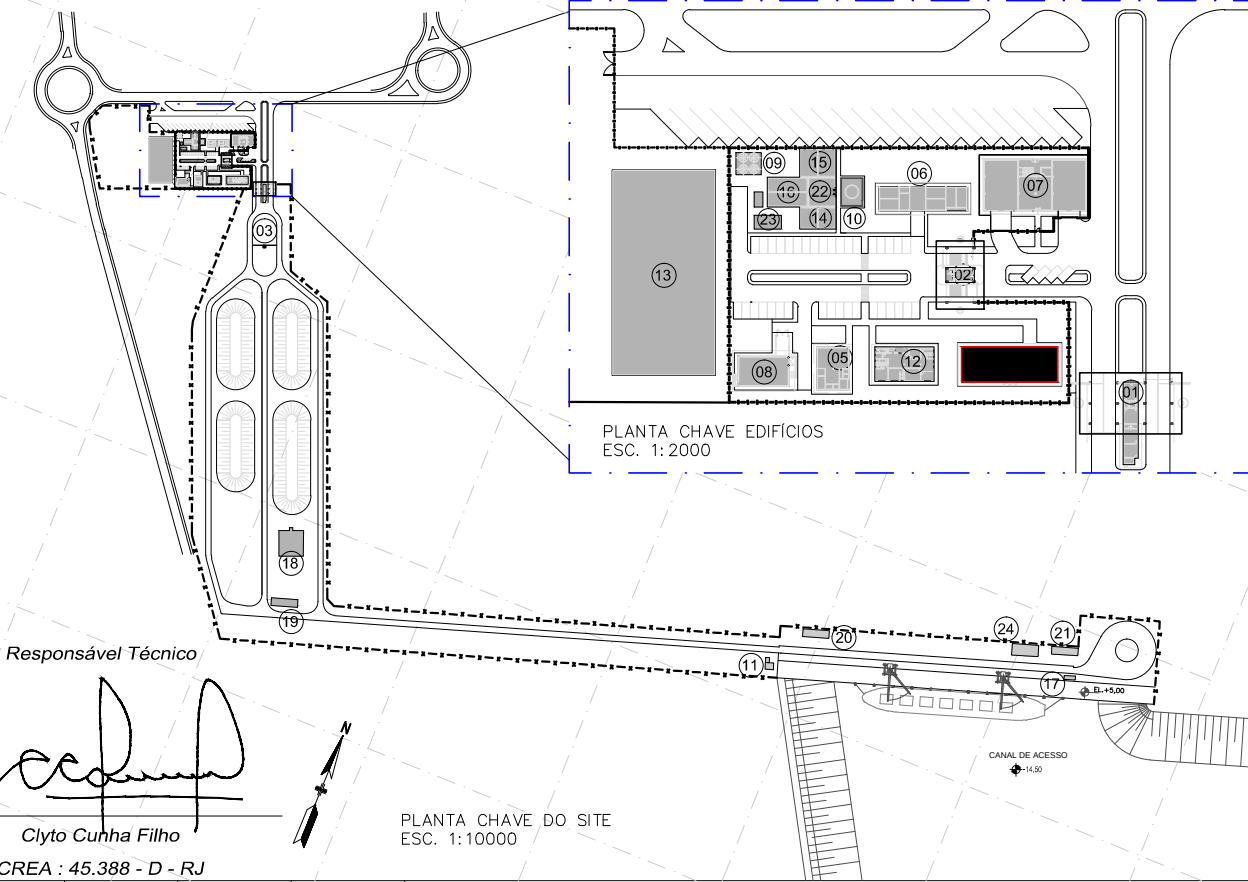

Responsável Técnico

Clyto Cunha Filho

CREA: 45.388-D-RJ

PLANTA CHAVE DO SITE
ESC. 1:10000

REV.	DATA	TIPO	POR	DESCRIÇÃO DAS REVISÕES
A	09/04/2015	E	EGS	ATENDIDO COMENTÁRIOS CONFORME GRD 071-15 - PARA CONSTRUÇÃO
D	22/01/2015	B	EGS	PARA COMENTÁRIOS

TIPO DE EMISSÃO	(A) PRELIMINAR (B) P/COMENTÁRIOS (C) P/CONHECIMENTO	(D) P/COTAÇÃO (E) P/CONSTRUÇÃO (F) CONFORME COMPRADO	(G) CONFORME CONSTRUÍDO (H) CANCELADO (I) APROVADO	(L) LIB. P/COMPRA (M) CERTIFICADO
-----------------	---	--	--	--------------------------------------

PRUMO LABORATÓRIO ENGENHARIA		AÇU OPERAÇÕES PORTUÁRIAS S/A	
engisique		PORTO DO AÇU - PROJETO EXECUTIVO INSTALAÇÕES ONSHORE - CIVIL T2 - TERMINAL DE MÚLTIPLO USO - TMULT - FASE I 04 - EDIFÍCIO ADMINISTRATIVO ARQUITETURA - PLANTA BAIXA	
RESPONSÁVEL	DATA	ESCALA	REV.
PROJ. ARQ.FICOTTO	16/01/2015	INDICADA	A
DES. ARQ.OLAVO	21/01/2015		
VERIF. ARQ.FICOTTO	22/01/2015		
APROV. ENG.CLYTO	22/01/2015		
No. PRU: AÇU-3.DES-2.3100-15-EGS-015		No. PROJETA: A1	