




04 EDIFÍCIO ADMINISTRATIVO
01 ELEVAÇÃO 01
ESC:ESC. 1:75

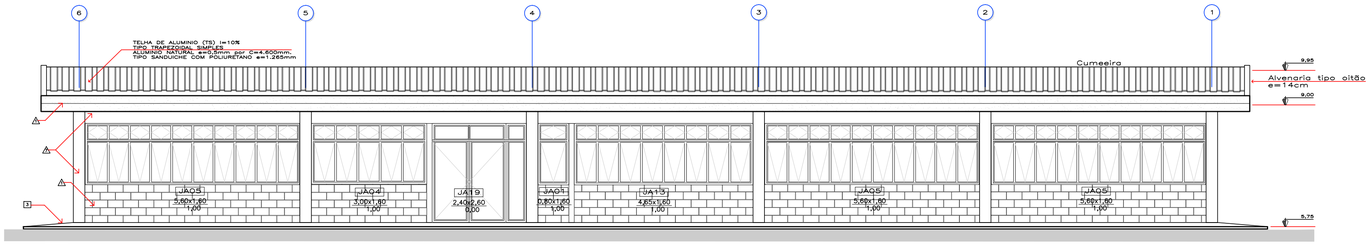


04 EDIFÍCIO ADMINISTRATIVO
03 ELEVAÇÃO 03
ESC:ESC. 1:75

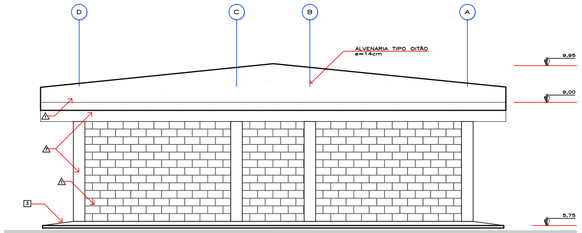


04 EDIFÍCIO ADMINISTRATIVO
04 ELEVAÇÃO 04
ESC:ESC. 1:75

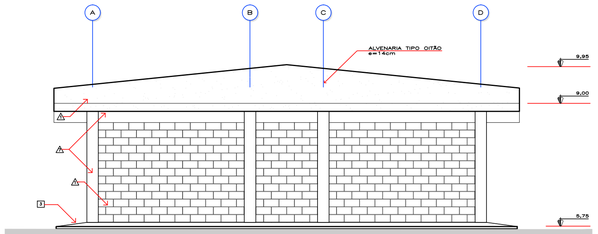

04 EDIFÍCIO ADMINISTRATIVO
02 ELEVAÇÃO 02
ESC:ESC. 1:75

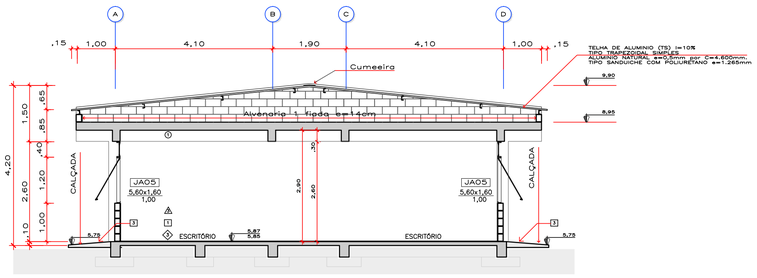

04 EDIFÍCIO ADMINISTRATIVO
CORTE B-B
ESC:ESC. 1:75

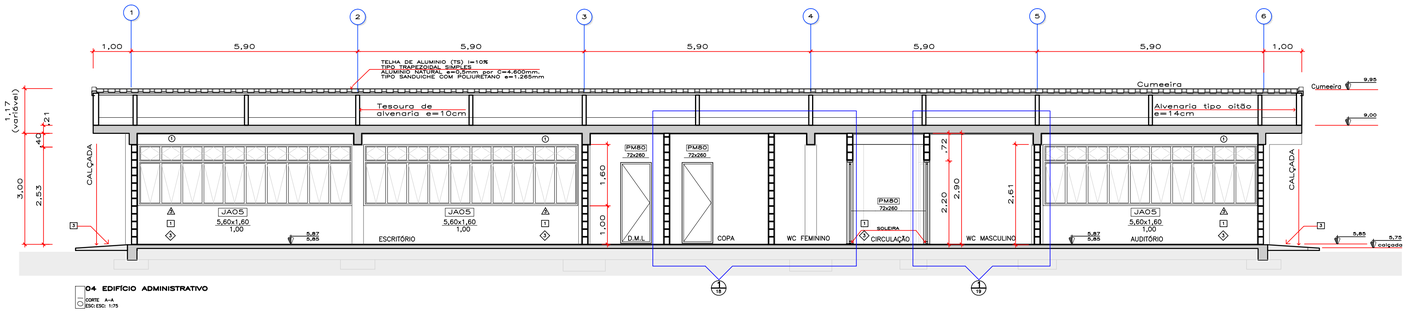

04 EDIFÍCIO ADMINISTRATIVO
CORTE A-A
ESC:ESC. 1:75

NOTAS

1– NÍVEIS, COORDENADAS E DIMENSÕES EM METRO.

2– AS ELEVAÇÕES INDICADAS REFEREM–SE AO ZERO DHN.
EL. DHN = EL. IBGE + 0,836 m.

3– COORDENADAS PLANAS UTM DATUM SAD 69.

4– VER TABELA DE ESQUADRIAS NA FOLHA: AÇU–3.DES–2.3100–15–EGS–089

5 – O SISTEMA DE AR CONDICIONADO PREVISTO SERÁ O SPLIT SYSTEM

DESENHOS DE REFERÊNCIA


Projeto básico do prédio administrativo. Folhas: AÇU–2.DES–2.3100–15–RAM–209 rev.B
AÇU–2.DES–2.3100–15–RAM–210 rev.B
Planta térreo: AÇU–3.DES–2.3100–15–EGS–015 rev.A

LEGENDA

LEGENDA DE ACABAMENTOS

	REVESTIMENTO PISO	
1	KORODUR – PISO DE ALTA RESISTÊNCIA, POLIDO, COR BEGE, COM JUNTAS METÁLICAS	
2	CERÂMICA ELIANE – MOD. CARGO PLUS GRAY 45x45 DE ALTO TRÁFEGO PEI–5 – ASSENTADO COM CIMENTO COLANTE ACIII CINZA – REJUNTE COM JUNTA 3mm COR PINUS FAB. ELIANE.	
3	PISO CIMENTADO LISO NO TRAÇO 1:3 DE CIMENTO E AREIA;	
4	CANCELADO	
5	CONTRAPISO DE CONCRETO POLIDO, CONF. PROJ. DE ESTRUTURA	
◇	**REVESTIMENTO PODAPÉ**	
1	CANCELADO	
2	MESMO MATERIAL APLICADO NA PAREDE	
3	RODAPÉ (H=10CM) EM GRANITO CINZA ANDORINHA.	
4	RODAPÉ (H=10CM) FAIXA DE CIMENTADO	
△	**REVESTIMENTO PAREDE**	
1	PINTURA PVA COR BEGE SOBRE BLOCOS DE CONCRETO APARENTE.	
2	PINTURA PVA BRANCA SOBRE ARGAMASSA.	
3	RODAPÉ (H=10CM) EM GRANITO CINZA ANDORINHA, SEGUIDO DE CERÂMICA ELIANE SLIM BRANCO 30x40CM, C/ JUNTAS 2mm COR BRANCO NEVE, ASSENTADO COM ARGAMASSA COLANTE ACIII CINZA, ATE ALTURA DE 1,80m. SEGUIDO DE RODA–MEIO (H=10CM) EM GRANITO CINZA ANDORINHA E ACIMA DISTO PINTURA PVA BRANCA SOBRE ARGAMASSA.	
4	CERÂMICA ELIANE, MOD. DIAMANTA BRANCO BRILHO,32,5x59, RETIFICADA, JUNTA 1mm C/ REJUNTE BRANCO EPOXI, ATÉ O TETO	
5	DIVISÓRIAS DE H=2,00m TOTAL, INSTALADA A 0,20m DO PISO, GRANITO CINZA ANDORINHA.	
6	DIVISÓRIAS COM REVESTIMENTO EM LAMINADO MELAMÍNICO NAS DUAS FACES.	
7	PINTURA COM VERNIZ POLIURETANO INCORLOR	
○	**REVESTIMENTO TETO**	
1	PINTURA EM TINTA PVA NA COR BRANCO NEVE SOBRE LAJE REBOCADA E EMBOÇO DESEMPENADO;	
2	PINTURA EM TINTA PVA NA COR BRANCO NEVE SOBRE MASSA PVA SOBRE FORRO EM GESSO COMUM, REMOVÍVEL	
3	COBERTURA EM ESTRUTURA ESPACIAL DE ALUMÍNIO ANODIZADO NATURAL COM EMPENA EM CHAPA CORRUGADA DE ALUMÍNIO ANODIZADO PRETO	
4	FORRO DE LAMBRI DE PVC BRANCO REMOVÍVEL LAVAVEL REGUA 10cm.	

PLANTA CHAVE

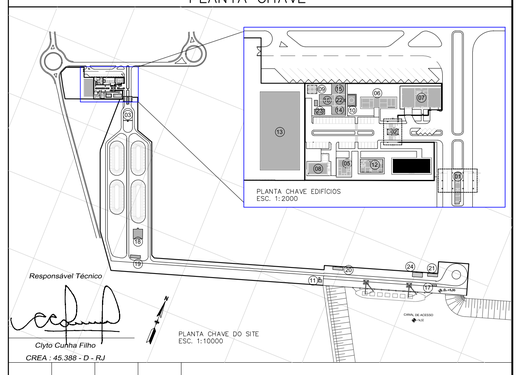

Responsável Técnico
Clyto Gunha Filho
CREA : 45.388 - D - RJ

REV.	DATA	TIPO	POR	DESCRIÇÃO DAS REVISÕES
A	09/04/2015	E	EGS	ATENDIDO COMENTÁRIOS CONFOME GRD 071–15 – PARA CONSTRUÇÃO
0	22/01/2015	B	EGS	EMISSÃO PARA COMENTÁRIOS

EMISSÕES

TIPO DE EMISSÃO

(A) PRELIMINAR
(B) P/COMENTÁRIOS
(C) P/CONHECIMENTO
(D) P/COTAÇÃO
(E) P/CONSTRUÇÃO
(F) CONFORME COMPRADO
(G) CONFORME CONSTRUIDO
(H) CANCELADO
(J) APROVADO
(L) LIB. P/COMPRA
(M) CERTIFICADO

PRUMO LOGÍSTICA GLOBAL
engesique

AÇU OPERAÇÕES PORTUARIAS S/A

PORTO DO AÇU – PROJETO EXECUTIVO
INSTALAÇÕES ONSHORE – CIVIL
T2 – TERMINAL DE MÚLTIPLO USO –TMULT – FASE I
04 – EDIFÍCIO ADMINISTRATIVO
ARQUITETURA – ELEVAÇÕES

RESPONSÁVEL		DATA
PROJ.	ARQ.FICOTTO	16/01/2015
DES.	ARQ.OLAVO	21/01/2015
VERIF.	ARQ.FICOTTO	22/01/2015
APROV.	ENG.CLYTO	22/01/2015

ESCALA INDICADA

No. PRL: AÇU–3.DES–2.3100–15–EGS–016 — REV. A

No. PROJETISTA:

FORMATO A1