


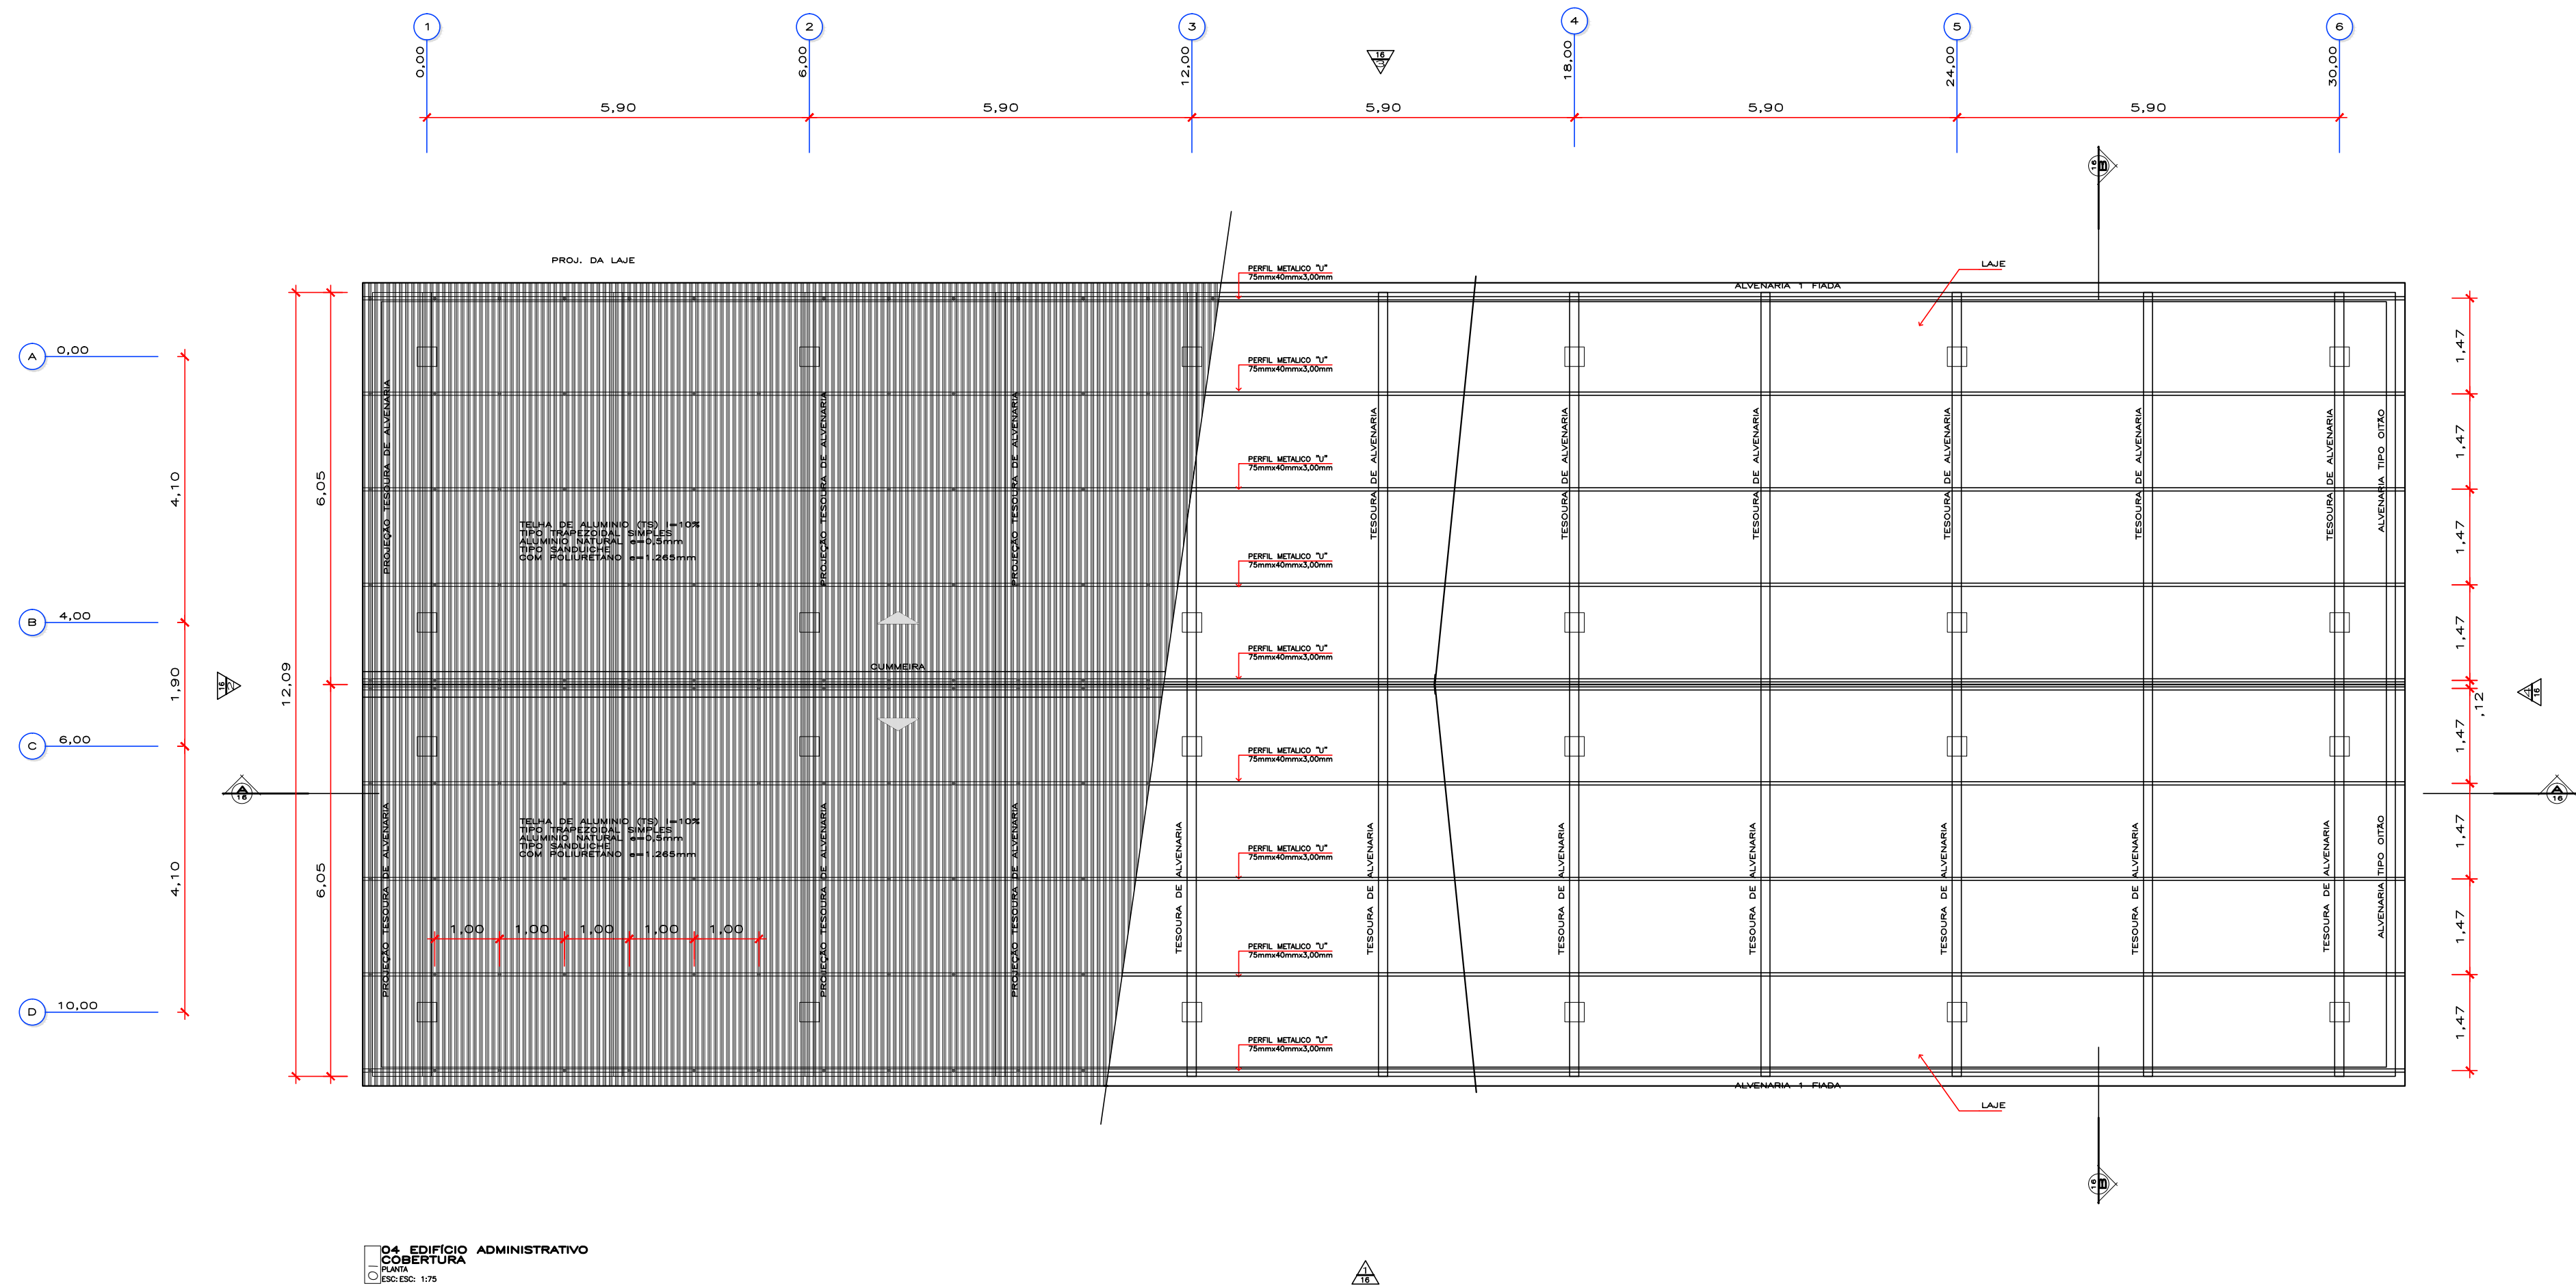

NOTAS


- 1- NIVEIS, COORDENADAS E DIMENSÕES EM METRO.
- 2- AS ELEVÇÕES INDICADAS REFEREM-SE AO ZERO DHN.
EL. DHN = EL. IBGE + 0,836 m.
- 3- COORDENADAS PLANAS UTM DATUM SAD 69.
- 4- VER TABELA DE ESQUADRIAS NA FOLHA: AQU-3.DES-2.3100-15-EGS-089
- 5 - O SISTEMA DE AR CONDICIONADO PREVISTO SERÁ O SPLIT SYSTEM

DESENHOS DE REFERÊNCIA

Projeto básico do prédio administrativo. Folhas: AQU-2.DES-2.3100-15-RAM-210 rev.B
AQU-2.DES-2.3100-15-RAM-211 rev.B
AQU-2.DES-2.3100-15-RAM-211 rev.B
Planta térreo: AQU-3.DES-2.3100-15-EGS-015 rev.A
Implantação: AQU-3.DES-2.3100-14-EGS-001 rev.0

LEGENDA

PLANTA CHAVE

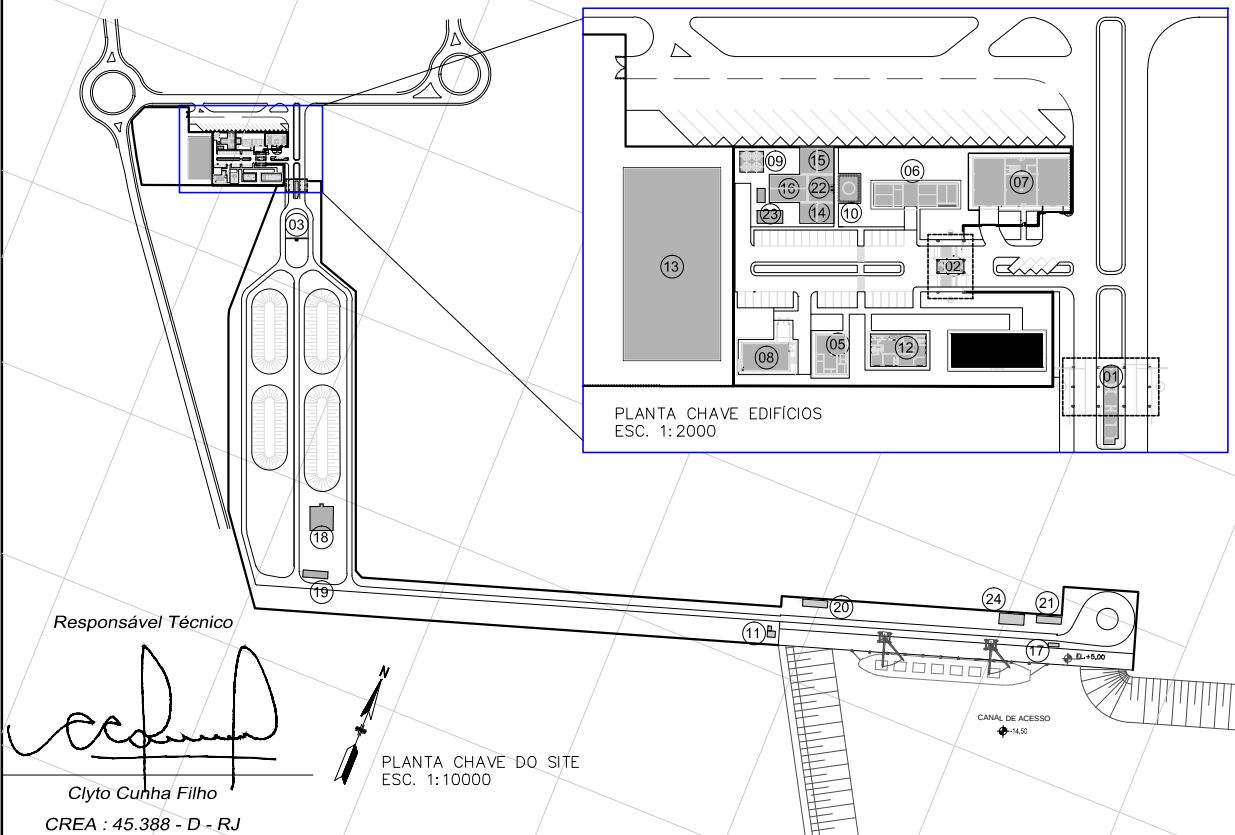

A	09/04/2015	E	EGS	ATENDIDO COMENTÁRIOS CONFORME GRD 071-15 - PARA CONSTRUÇÃO	
0	16/01/2015	B	EGS	EMISSÃO PARA COMENTÁRIOS	
REV.	DATA	TIPO	POR	DESCRIÇÃO DAS REVISÕES	
EMISSÕES					
TIPO DE EMISSÃO	(A) PRELIMINAR		(D) P/OTAÇÃO	(G) CONFORME CONSTRUÍDO	(L) LIB. P/COMPRA
	(B) P/COMENTÁRIOS		(E) P/CONSTRUÇÃO	(H) CANCELADO	(M) CERTIFICADO
	(C) P/CONHECIMENTO		(F) CONFORME COMPRADO	(I) APROVADO	
			AÇU OPERAÇÕES PORTUARIAS S/A		
			PORTO DO AÇU - PROJETO EXECUTIVO		
			INSTALAÇÕES ONSHORE - CIVIL		
			T2 - TERMINAL DE MÚLTIPLO USO -TMULT - FASE I		
			04 - EDIFÍCIO ADMINISTRATIVO		
			PLANTA - COBERTURA		
RESPONSÁVEL			DATA		
PROJ.	ARQ.FICOTTO	16/01/2015			
DES.	ARQ.OLAVO	16/01/2015			
VERIF.	ARQ.FICOTTO	16/01/2015			
APROV.	ENG.CLYTO	16/01/2015			
ESCALA			NO. PRL: AQU-2.3100-15-EGS-017	REV. A	
INDICADA			NO. PROJETISTA:	FORMATO A1	