



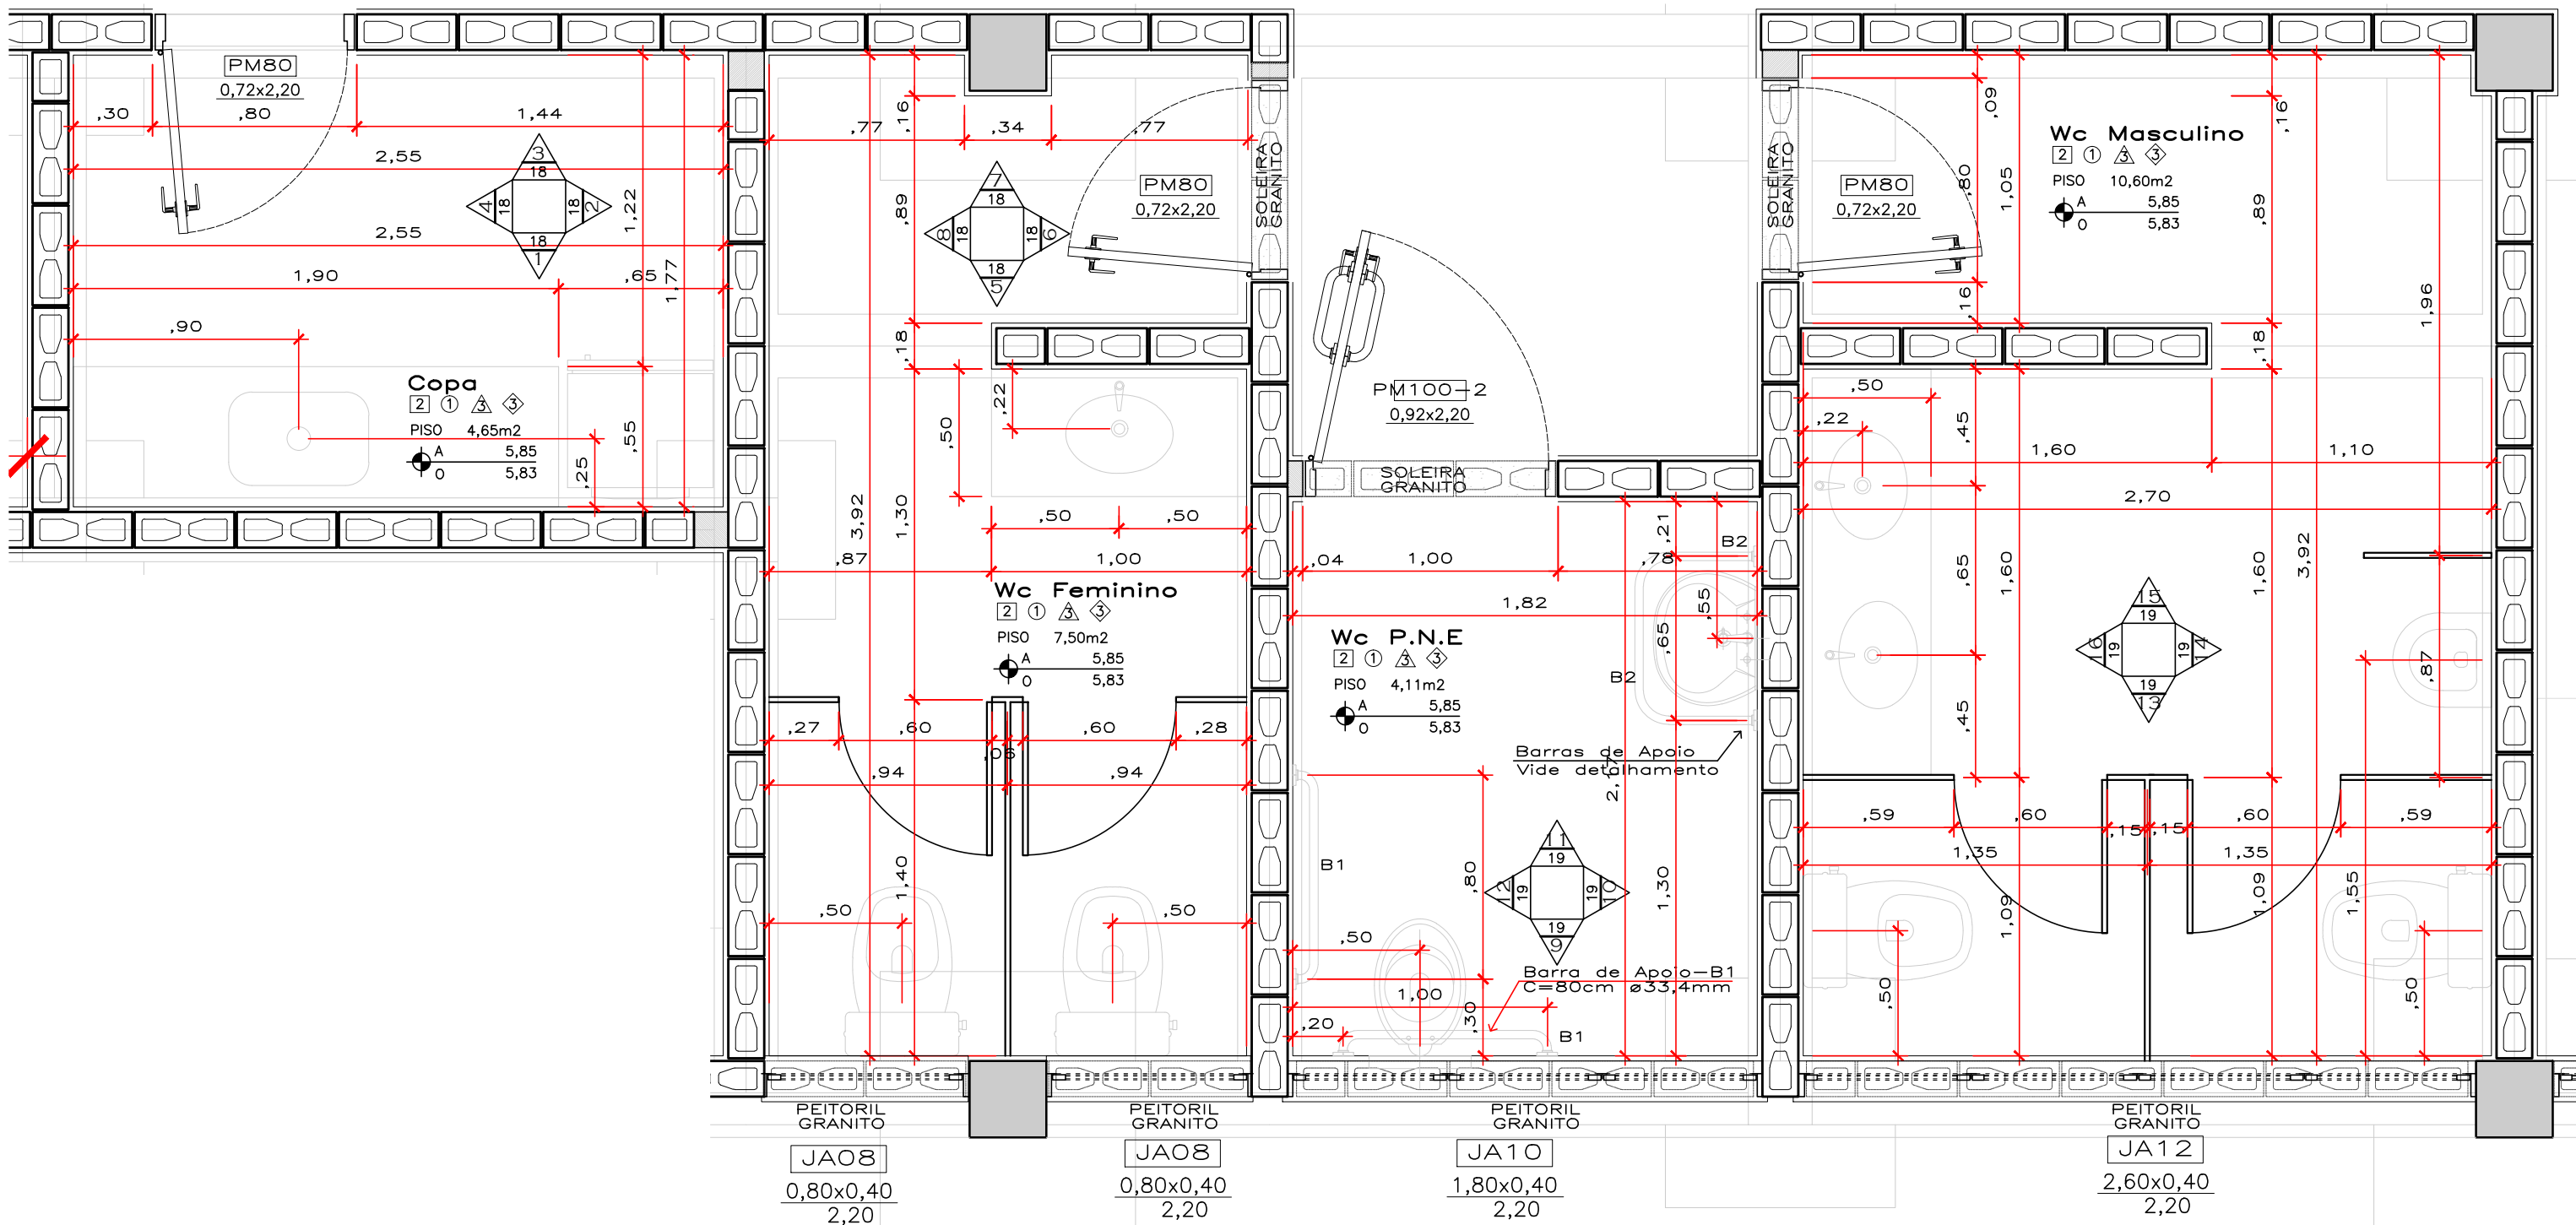


04 EDIFÍCIO ADMINISTRATIVO
COPA — EL. 01
AMPLIAÇÃO
PLANTA BAIXA
ESC: 1:25


LIMITE CALÇADA
PROJEÇÃO COBERTURA

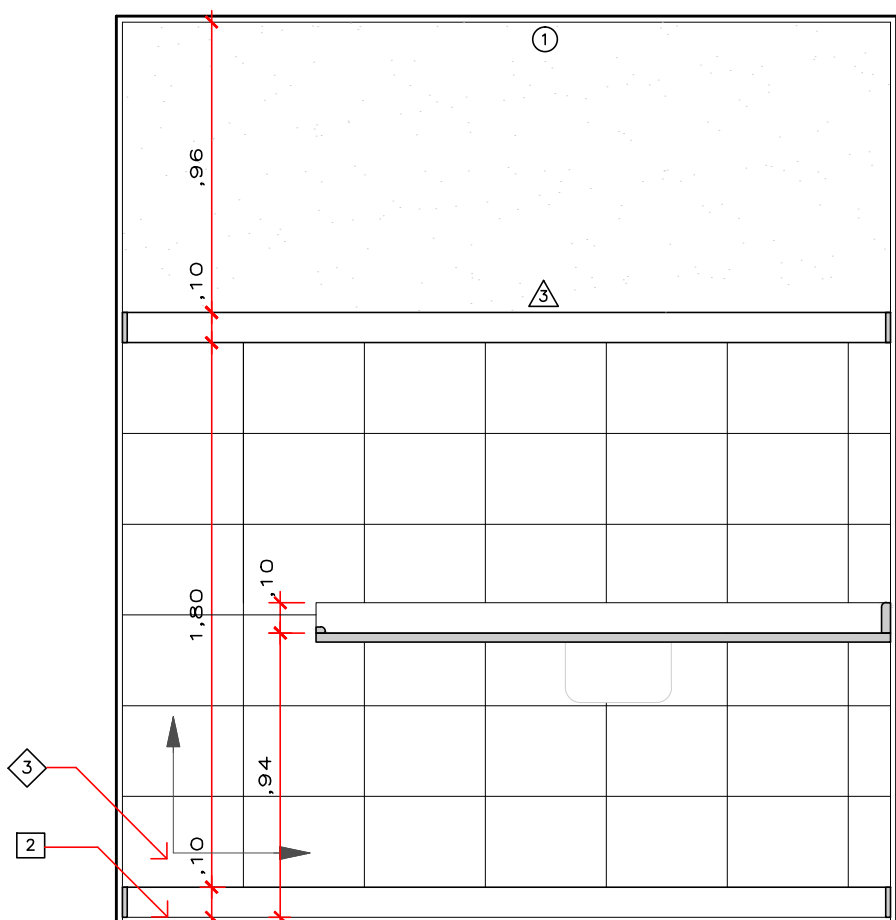


04 EDIFÍCIO ADMINISTRATIVO
COPA — EL. 01
AMPLIAÇÕES
ESC: ESC: 1:25

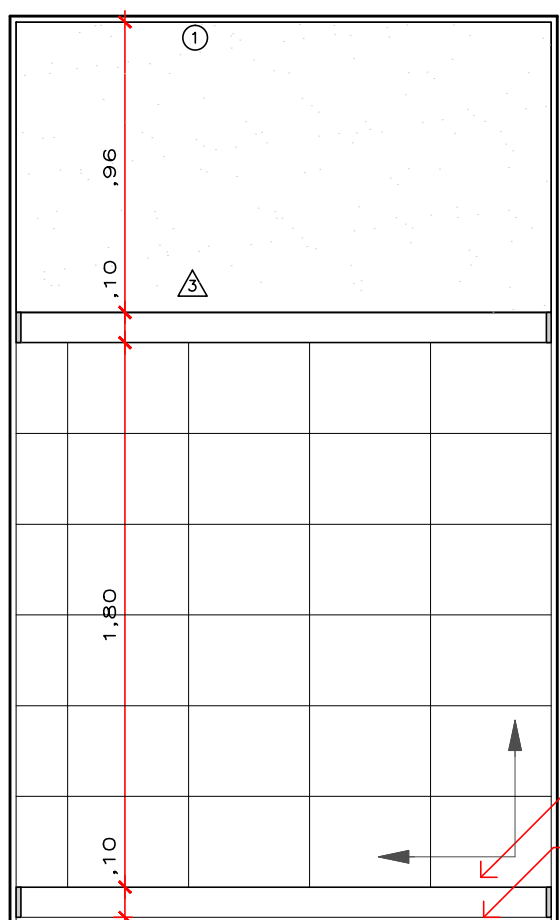

04 EDIFÍCIO ADMINISTRATIVO
COPA — EL. 02
AMPLIAÇÕES
ESC: ESC: 1:25

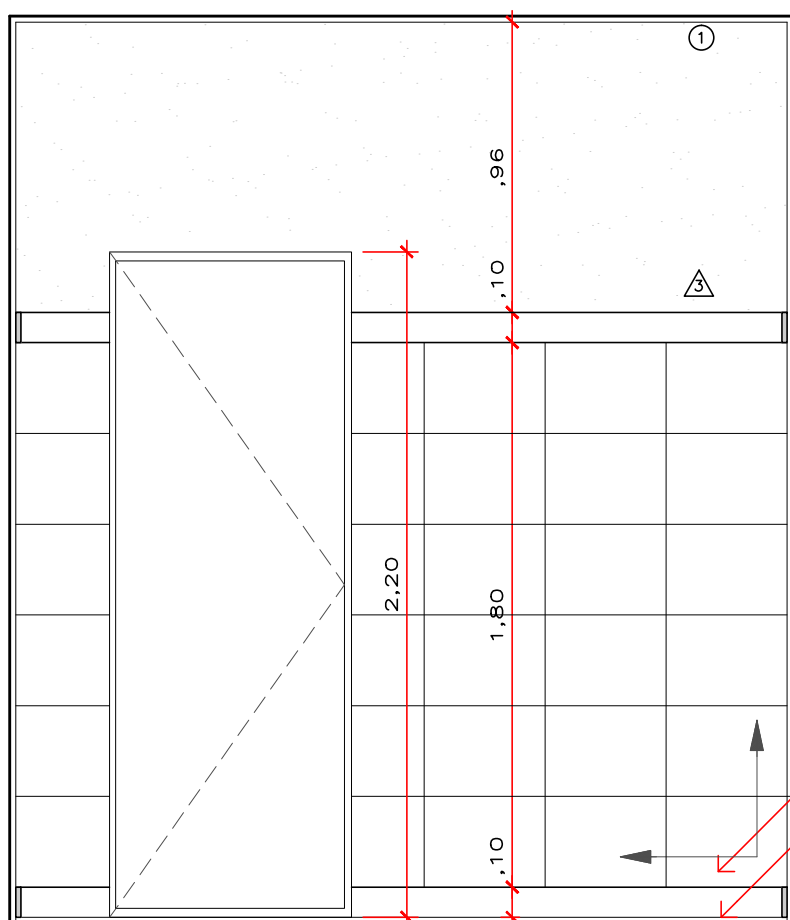

04 EDIFÍCIO ADMINISTRATIVO
COPA — EL. 03
AMPLIAÇÕES
ESC: ESC: 1:25

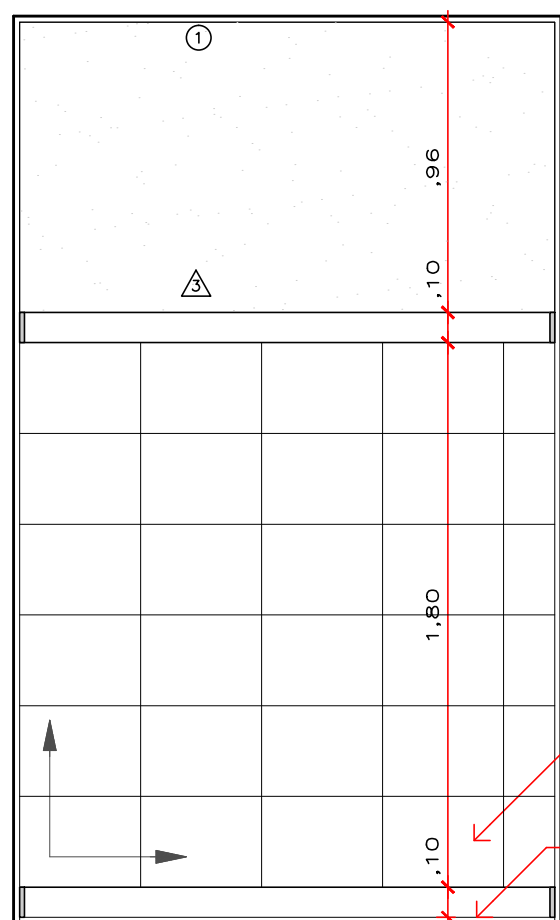

04 EDIFÍCIO ADMINISTRATIVO
COPA — EL. 04
AMPLIAÇÕES
ESC: ESC: 1:25

NOTAS

- 1- NIVEIS, COORDENADAS E DIMENSÕES EM METRO.
- 2- AS ELEVACÕES INDICADAS REFEREM-SE AO ZERO DHN.
EL. DHN = EL. IBGE + 0,836 m.
- 3- COORDENADAS PLANAS UTM DATUM SAD 69.
- 4- VER TABELA DE ESQUADRIAS NA FOLHA: AÇU-3.DES-2.3100-15-EGS-089
- 5 - O SISTEMA DE AR CONDICIONADO PREVISTO SERÁ O SPLIT SYSTEM

DESENHOS DE REFERÊNCIA


Implantação: AÇU-3.DES-2.3100-14-EGS-001 rev.0
Planta térreo: AÇU-3.DES-2.3100-15-EGS-015 rev.A
Cortes: AÇU-3.DES-2.3100-15-EGS-016 rev.A

LEGENDA

LEGENDA DE ACABAMENTOS

REVESTIMENTO PISO
1 KORODUR — PISO DE ALTA RESISTÊNCIA, POLIDO, COR BEGE, COM JUNTAS METÁLICAS
2 CERÂMICA ELIANE — MOD. CARO PLUS GRAY 45x45 DE ALTO TRÁFEGO PI-5 — ASSENTADO COM CIMENTO COLANTE ACIII CINZA — REJUNTE COM JUNTA 3mm COR PINUS FAB. ELIANE.
3 PISO CIMENTADO LISO NO TRAÇO 1:3 DE CIMENTO E AREIA;
4 CANCELADO
5 CONTRAPISSO DE CONCRETO POLIDO, CONF. PROJ. DE ESTRUTURA
REVESTIMENTO RODAPÉ
1 CANCELADO
2 MESMO MATERIAL APLICADO NA PAREDE
3 RODAPÉ (H=10CM) EM GRANITO CINZA ANDORINHA.
4 RODAPÉ (H=10CM) FAIXA DE CIMENTADO
REVESTIMENTO PAREDE
1 PINTURA PVA COR BEGE SOBRE BLOCOS DE CONCRETO APARENTE.
2 PINTURA PVA BRANCA SOBRE ARGAMASSA.
3 RODAPÉ (H=10CM) EM GRANITO CINZA ANDORINHA, SEGUIDO DE CERÂMICA ELIANE SUM BRANCO 30x40CM, C/ JUNTAS 2mm COR BRANCO NEVE, ASSENTADO COM ARGAMASSA COLANTE ACIII CINZA, ATE ALTURA DE 1,80m. SEGUIDO DE RODA-MEIO (H=10CM) EM GRANITO CINZA ANDORINHA E ACIMA DISSO PINTURA PVA BRANCA SOBRE ARGAMASSA.
4 CERÂMICA ELIANE, MOD. DIAMANTA BRANCO BRILHO,32,5x59, RETIFICADA, JUNTA 1mm C/ REJUNTE BRANCO EPOXI, ATE O TETO
5 DIVISÓRIAS DE H=2,00m TOTAL, INSTALADA A 0,20m DO PISO. GRANITO CINZA ANDORINHA.
6 DIVISÓRIAS COM REVESTIMENTO EM LAMINADO MELAMINICO NAS DUAS FACES.
7 PINTURA COM VERNIZ POLIURETANO INCORLOR
REVESTIMENTO TETO
1 PINTURA EM TINTA PVA NA COR BRANCO NEVE SOBRE LAJE REBOCADA E EMBOÇO DESEMPENADO;
2 PINTURA EM TINTA PVA NA COR BRANCO NEVE SOBRE MASSA PVA SOBRE FORRO EM GESSO COMUM, REMOVIVEL
3 COBERTURA EM ESTRUTURA ESPACIAL DE ALUMÍNIO ANODIZADO NATURAL COM EMPENA EM CHAPA CORRUGADA DE ALUMÍNIO ANODIZADO PRETO
4 FORRO DE LAMBRI DE PVC BRANCO REMOVIVEL LAVAVEL REGUA 10cm.

PLANTA CHAVE

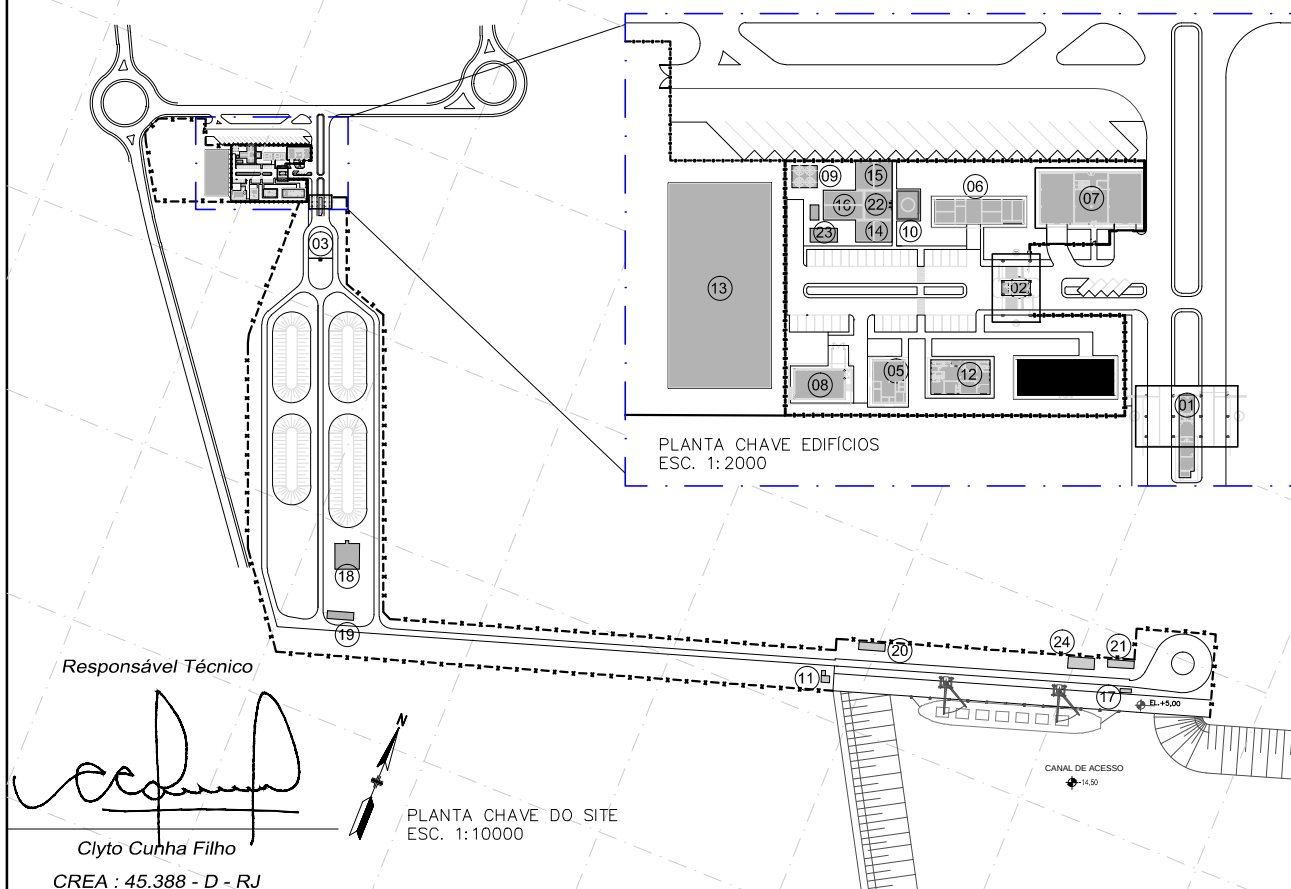

Responsável Técnico

Clyto Cunha Filho

CREA : 45.388 - D - RJ

PLANTA CHAVE DO SITE
ESC: 1:10000

CREA : 45.388 - D - RJ

REV.	DATA	TIPO	POR	DESCRIÇÃO DAS REVISÕES
A	17/03/2015	E	EGS	ATENDIDO COMENTÁRIOS CONFORME GRD 093-15 — PARA APROVAÇÃO
D	22/01/2015	B	EGS	EMIÇÃO INICIAL PROJETO EXECUTIVO

TIPO DE EMISSÃO	(A) PRELIMINAR (B) P/COMENTÁRIOS (C) P/CONHECIMENTO	(D) P/COTAÇÃO (E) P/CONSTRUÇÃO (F) CONFORME COMPRADO	(G) CONFORME CONSTRUÍDO (H) CANCELADO (I) APROVADO	(L) LIB. P/COMPRA (M) CERTIFICADO
-----------------	---	--	--	--------------------------------------

PRUMO LABORATÓRIO ENGENHARIA		AÇU OPERAÇÕES PORTUÁRIAS S/A	
engiesique		PORTO DO AÇU — PROJETO EXECUTIVO INSTALAÇÕES ONSHORE — CIVIL T2 — TERMINAL DE MÚLTIPLO USO —TULT — FASE I 04 — EDIFÍCIO ADMINISTRATIVO ARQUITETURA — AMPLIAÇÃO FL. 01/02	
RESPONSÁVEL	DATA	ESCALA	REV.
PROJ. ARQ.FICOTTO	16/01/2015	INDICADA	A
DES. ARQ.OLAVO	21/01/2015		
VERIF. ARQ.FICOTTO	22/01/2015		
APROV. ENG.CLYTO	22/01/2015		
No. PRL: AÇU-3.DES-2.3100-15-EGS-018		No. PROJETA: A	
FORMATO A1			