


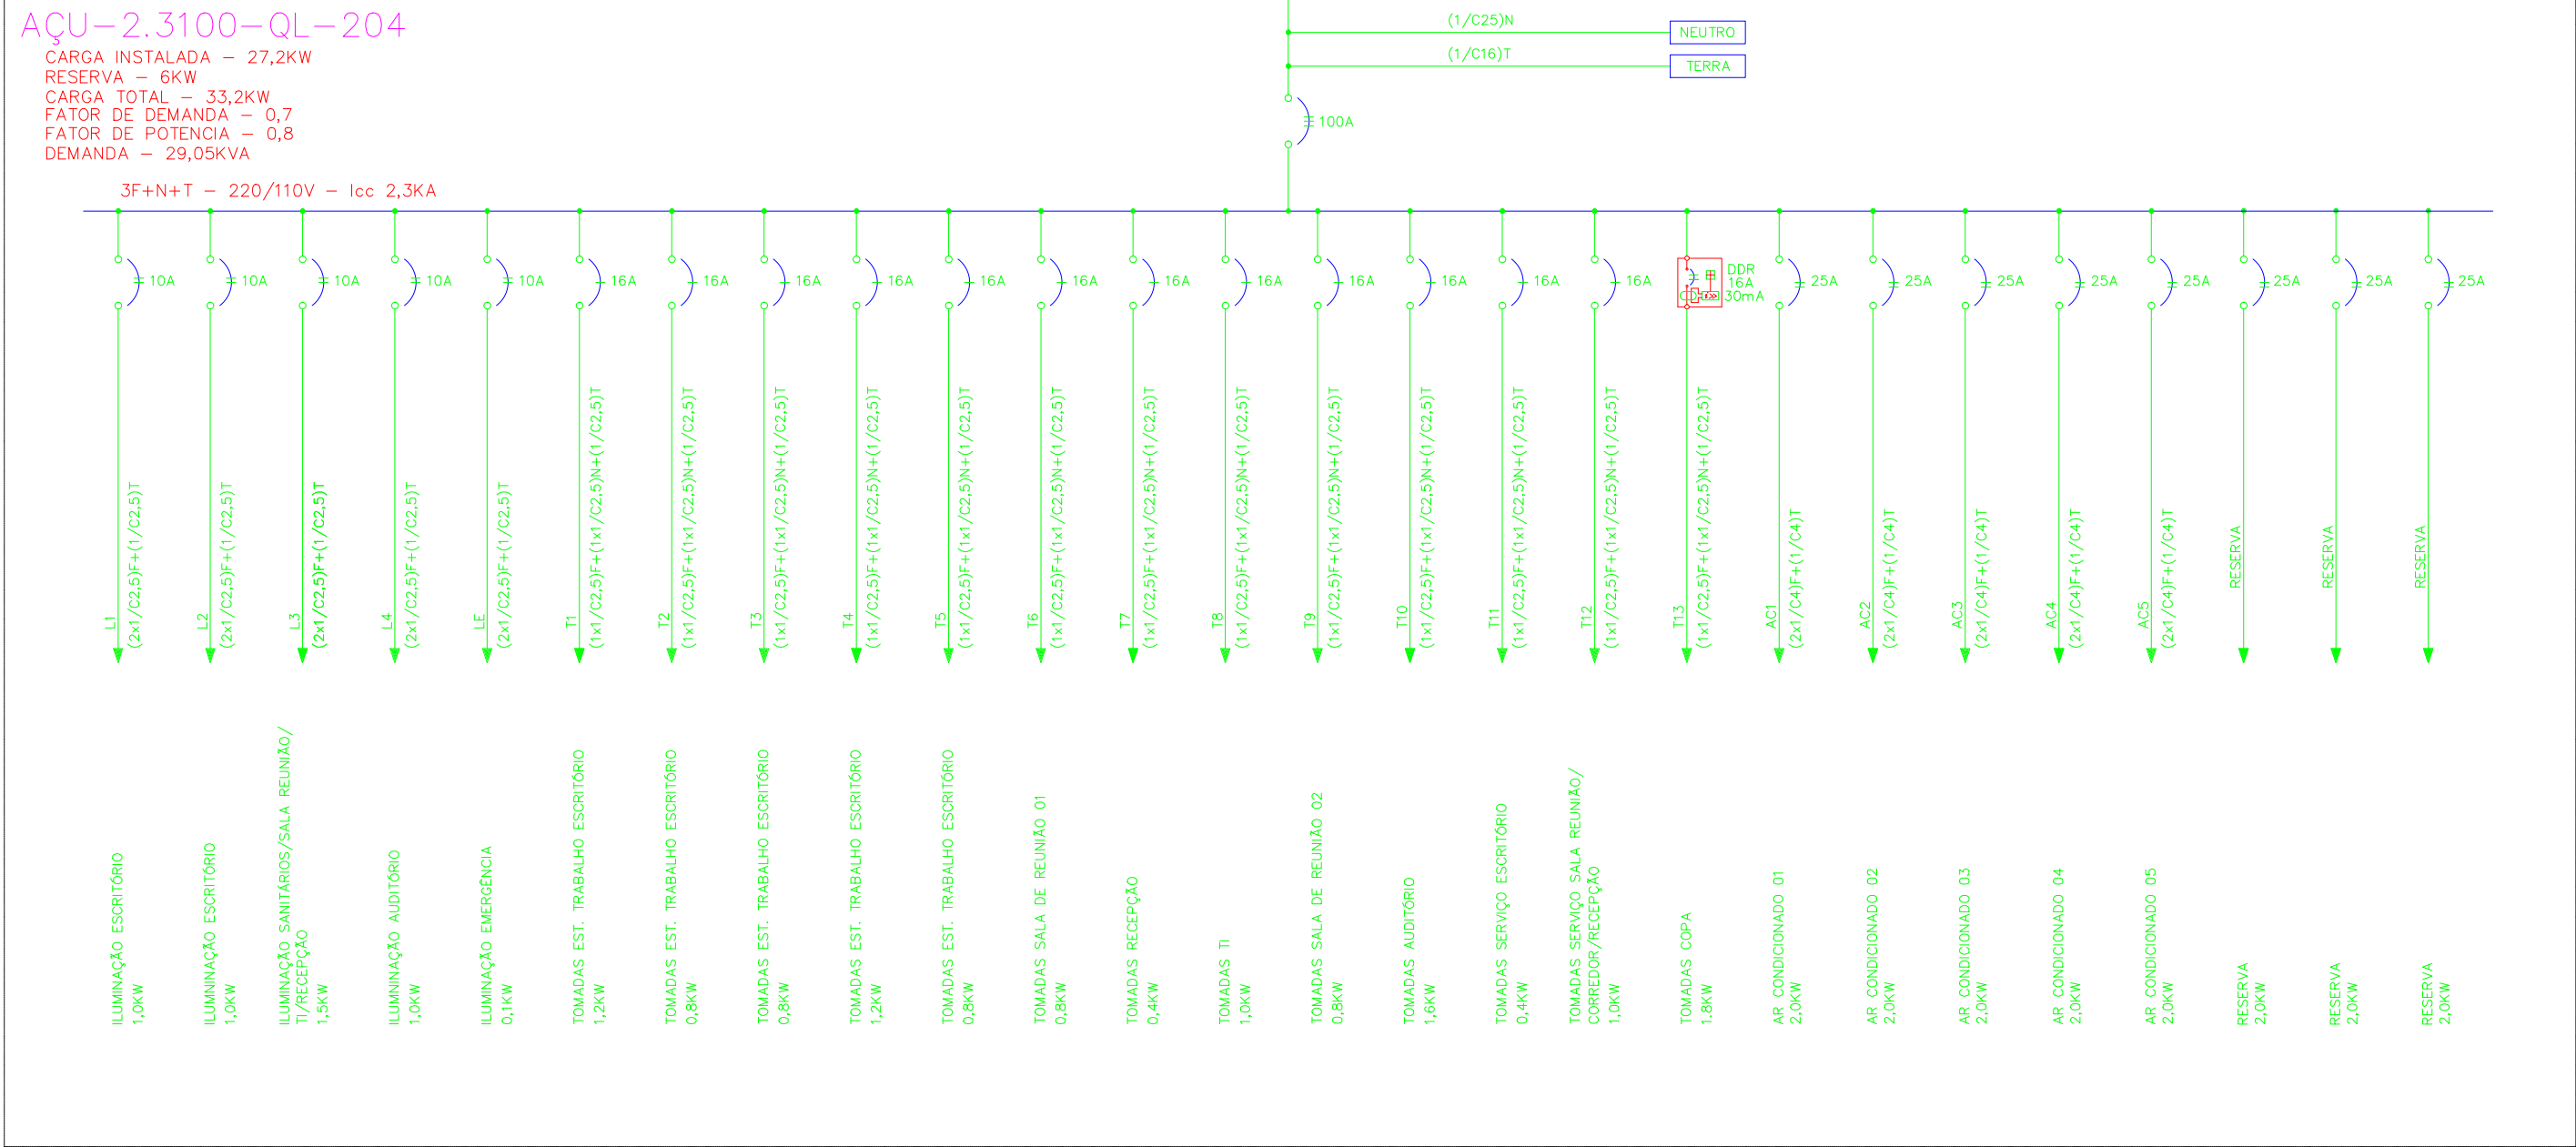

04 EDIFÍCIO ADMINISTRATIVO
QUADRO DE ILUMINAÇÃO
DIAGRAMA UNIFILAR
ESC: S/ESC.

- NOTAS
- 1- QUADRO PARA INSTALAÇÃO ABRIGADA - GRAU DE PROTEÇÃO MÍNIMO IP-30.
 - 2- QUADRO CONFORME NBR IEC 60.439-3.
 - 3- OS DISJUNTORES DEVERÃO SER CONFORME NORMA NBR IEC 60497-2, DO TIPO CAIXA MOLDADA PARA ENTRADA E TIPO MINIDISJUNTOR PARA CIRCUITOS DE SAÍDA. CAPACIDADE DE INTERRUPÇÃO MÍNIMA DE CORRENTE DE CURTO-CIRCUITO DE 10KA.
 - 4- O QUADRO DEVERÁ SER METÁLICO, TIPO INDUSTRIAL, COM PORTA COM FECHO TIPO FENDA METÁLICO, COM DISPOSITIVO DE BLOQUEIO, COM ANTEPARO REMOVÍVEL SOMENTE COM AUXÍLIO DE FERRAMENTA.
 - 5- DEVERÁ SER FORNECIDO DISPOSITIVO DE BLOQUEIO PARA O DISJUNTOR GERAL.
 - 6- OS CIRCUITOS DEVERÃO SER IDENTIFICADOS, CONFORME O DIAGRAMA UNIFILAR, ATRAVÉS DE PLAQUETAS DE ACRÍLICO, COM LETRAS BRANCAS E FUNDO PRETO.
 - 7- TODOS OS QUADROS DEVERÃO TER PLACA DE CARACTERÍSTICAS EM AÇO INOX CONFORME O ITEM 5 DA NORMA NBR IEC 60.439-1/3.
 - 8- DEVERÁ SER FORNECIDO PROJETO DO QUADRO PARA APROVAÇÃO ANTES DA FABRICAÇÃO.
 - 9- ESTES DESENHOS FORAM ELABORADOS POR MEIOS ELETRÔNICOS. FICA PROIBIDA A REPRODUÇÃO DE PARTE OU TOTALIDADE DO MESMO SEM AUTORIZAÇÃO PRÉVIA DO AUTOR DO PROJETO. AS CÓPIAS DESTES DESENHOS SÃO VÁLIDAS DESDE QUE CONTENHAM A ASSINATURA DO ENGENHEIRO ELETRICISTA RESPONSÁVEL PELO PROJETO.

DESENHOS DE REFERÊNCIA

AÇU-3.DES-2.3100-16-EGS-013 - PRÉDIO ADMINISTRATIVO - 04 - INST. ELÉTRICAS
AÇU-3.ETE-2.3100-73-EGS-005 - ESPECIFICAÇÃO TÉCNICA - QUADROS DE ILUMINAÇÃO
AÇU-3.FDA-2.3100-73-EGS-003 - FOLHA DE DADOS - QUADROS DE ILUMINAÇÃO

LEGENDA

- 16A
DISJUNTOR TERMOMAGNÉTICO MONOPOLAR COM INDICAÇÃO DA CORRENTE NOMINAL
- 16A
DISJUNTOR TERMOMAGNÉTICO BIPOLAR COM INDICAÇÃO DA CORRENTE NOMINAL
- 16A
DISJUNTOR TERMOMAGNÉTICO TRIPOLAR COM INDICAÇÃO DA CORRENTE NOMINAL
- DDR 16A 30mA
DISJUNTOR DIFERENCIAL-RESIDUAL BIPOLAR COM INDICAÇÃO DA CORRENTE NOMINAL E DA CORRENTE DE FUGA
- DDR 16A 30mA
DISJUNTOR DIFERENCIAL-RESIDUAL TETRAPOLAR COM INDIC. DA CORRENTE NOMINAL E DA CORRENTE DE FUGA
- DISPOSITIVO DE BLOQUEIO (LOTO)
- MANOPLA DE AÇIONAMENTO DO DISJUNTOR NA PORTA DO QUADRO
- CHAVE COMUTADORA 2 POSIÇÕES 10A/250V

Responsável Técnico

Clyto Cunha Filho
CREA : 45.388 - D - RJ

0	06/02/15	8	LMX	EMISSÃO ORIGINAL
REV.	DATA	TIPO	POR	DESCRIÇÃO DAS REVISÕES
EMISSÕES				
TIPO DE EMISSÃO	(A) PRELIMINAR (B) P/COMENTÁRIOS (C) P/CONHECIMENTO			
	(D) P/COTAÇÃO (E) P/CONSTRUÇÃO (F) CONFORME COMPRADO			
	(G) CONFORME CONSTRUÍDO (H) CANCELADO (I) APROVADO			
	(J) US. P/COMPR (M) CERTIFICADO			
PRUMO		AÇU OPERAÇÕES PORTUARIAS S/A		
engesique		SUPERPORTO DO AÇU - PROJETO BÁSICO		
RESPONSÁVEL	DATA	INSTALAÇÕES ON SHORE - GERAL		
PROJ. LMX	06/02/15	T2 - TERMINAL DE MÚLTIPLO USO - TMULT - FASE I		
DES. GRM	06/02/15	INSTALAÇÕES ELÉTRICAS		
VERIF. ENG.RODRIGO	06/02/15	ESCALA	PRÉDIO ADMINISTRATIVO - QUADRO DE ILUMINAÇÃO	
APROV. ENG.CLYTO	06/02/15	S/ESC.	No. PROJ: AÇU-3.DES-2.3100-16-EGS-015	REV. 00
			No. PROJETISTA:	FORMATO A1