



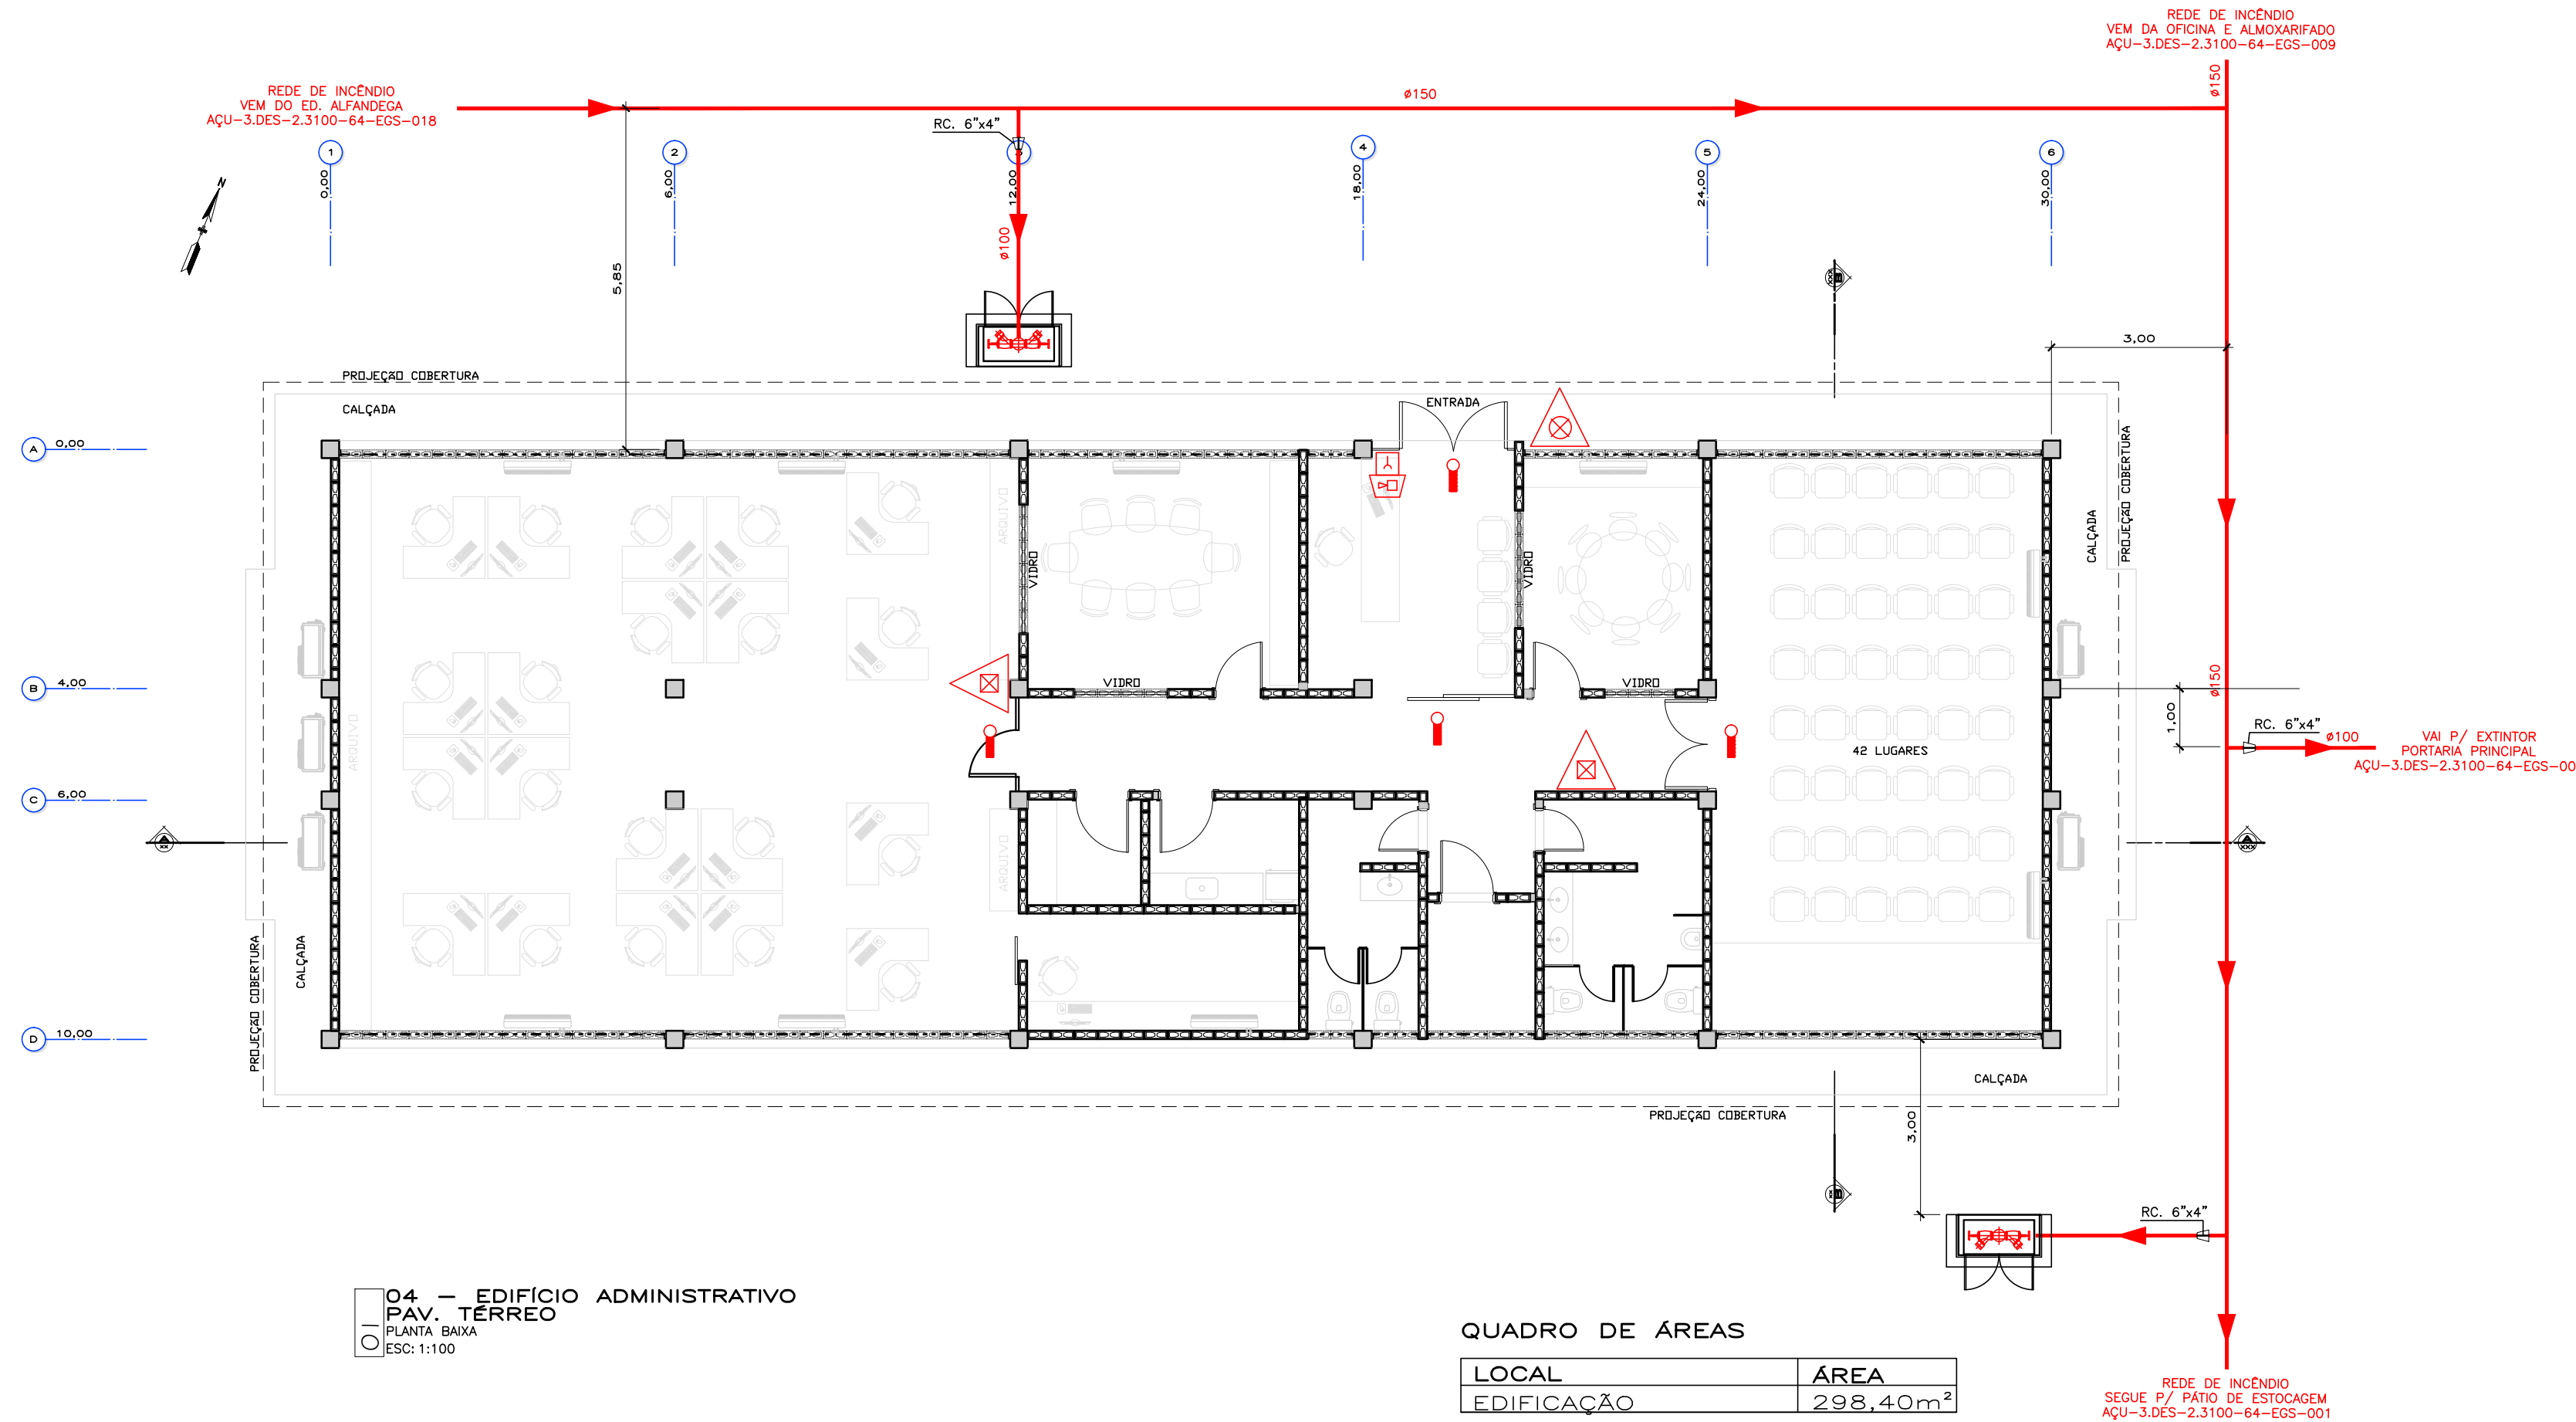


04 - EDIFÍCIO ADMINISTRATIVO
PAV. TÉRREO
PLANTA BAIXA
ESC: 1:100

QUADRO DE ÁREAS	
LOCAL	ÁREA
EDIFICAÇÃO	298,40m ²

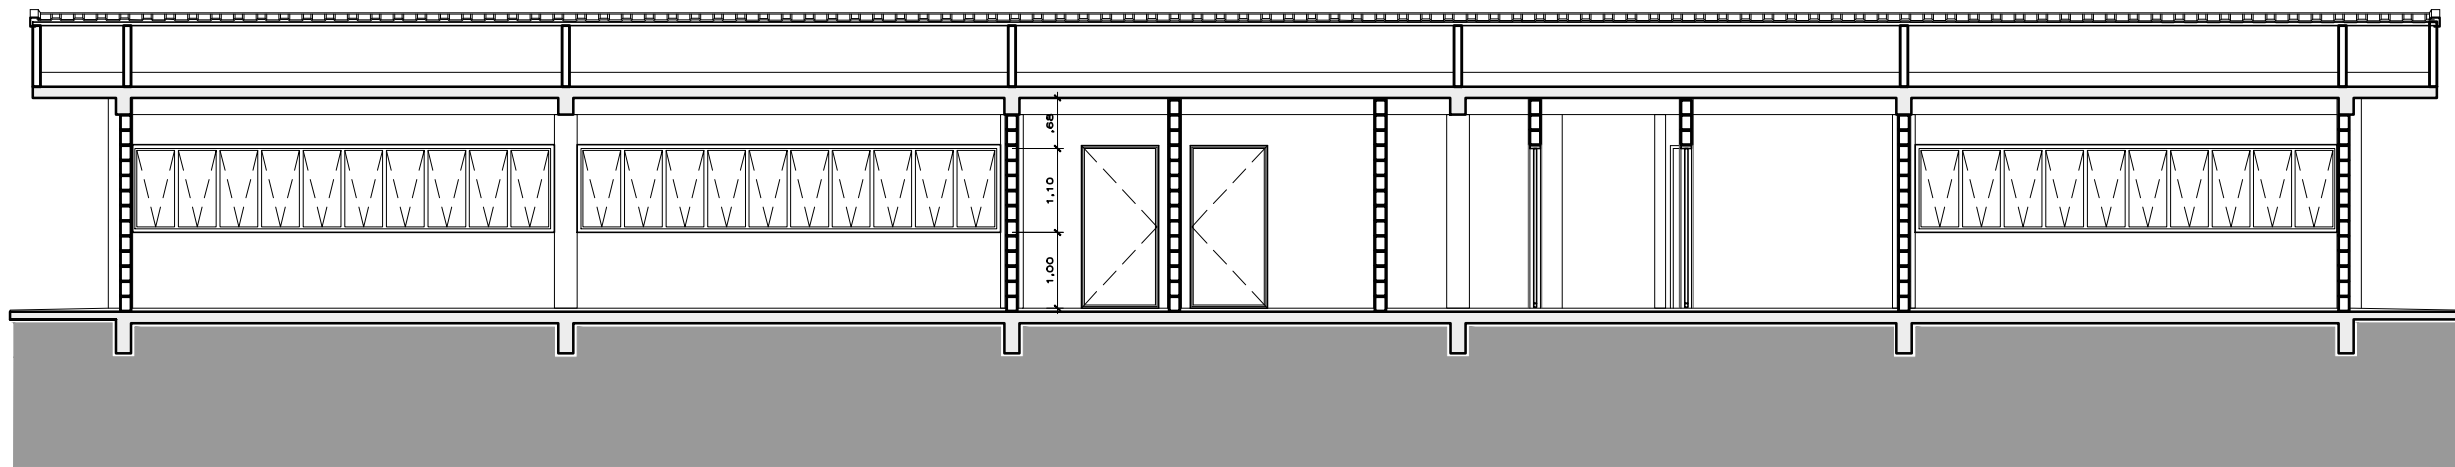

CORTE A-A

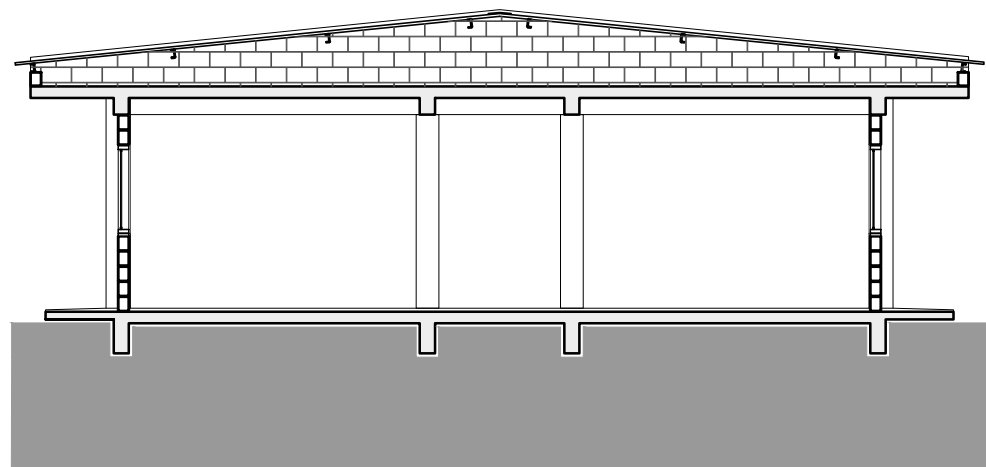

CORTE B-B


NOTAS

- 1- NÍVEIS E DIMENSÕES EM METRO. DIÂMETRO DAS TUBULAÇÕES EM MILÍMETRO, SALVO INDICAÇÃO CONTRÁRIA.
- 2- REDES E RAMAIS EM AÇO CARBONO COM PROTEÇÃO CONTRA CORROSÕES ADEQUADAS PARA AS CONDIÇÕES FÍSICAS LOCAIS.
- 3- PARA DETALHES, VER DES. AÇU-3.DES-2.3100.64.EGS.002

LEGENDA

- REDE E RAMAIS DE COMBATE A INCENDIO
- SENTIDO DO FLUXO
- REDUÇÃO NO TUBO
- HIDRANTE DE COLUMNA DUPLO 500L/min CADA SAÍDA (CL RISCO B)
- DIÂMETRO DO TUBO
- VÁLVULAS DE CENTRO
- VÁLVULA DE GAVETA
- CAIXA DE MATERIAL DE COMBATE A INCENDIO
- EXTINTOR DE PÓ QUÍMICO SECO BC
- EXTINTOR DE ÁGUA PRESSURIZADA
- PONTO DE ILUMINAÇÃO DE EMERGÊNCIA DE BLOCO
- CENTRAL DE ALARME
- ACIONADOR MANUAL DO SISTEMA DE ALARME
- AVISADOR SONORO TIPO SIRENE
- RESERVA DE INCENDIO
- HIDRANTE DUPLO NA PAREDE

PLANTA CHAVE

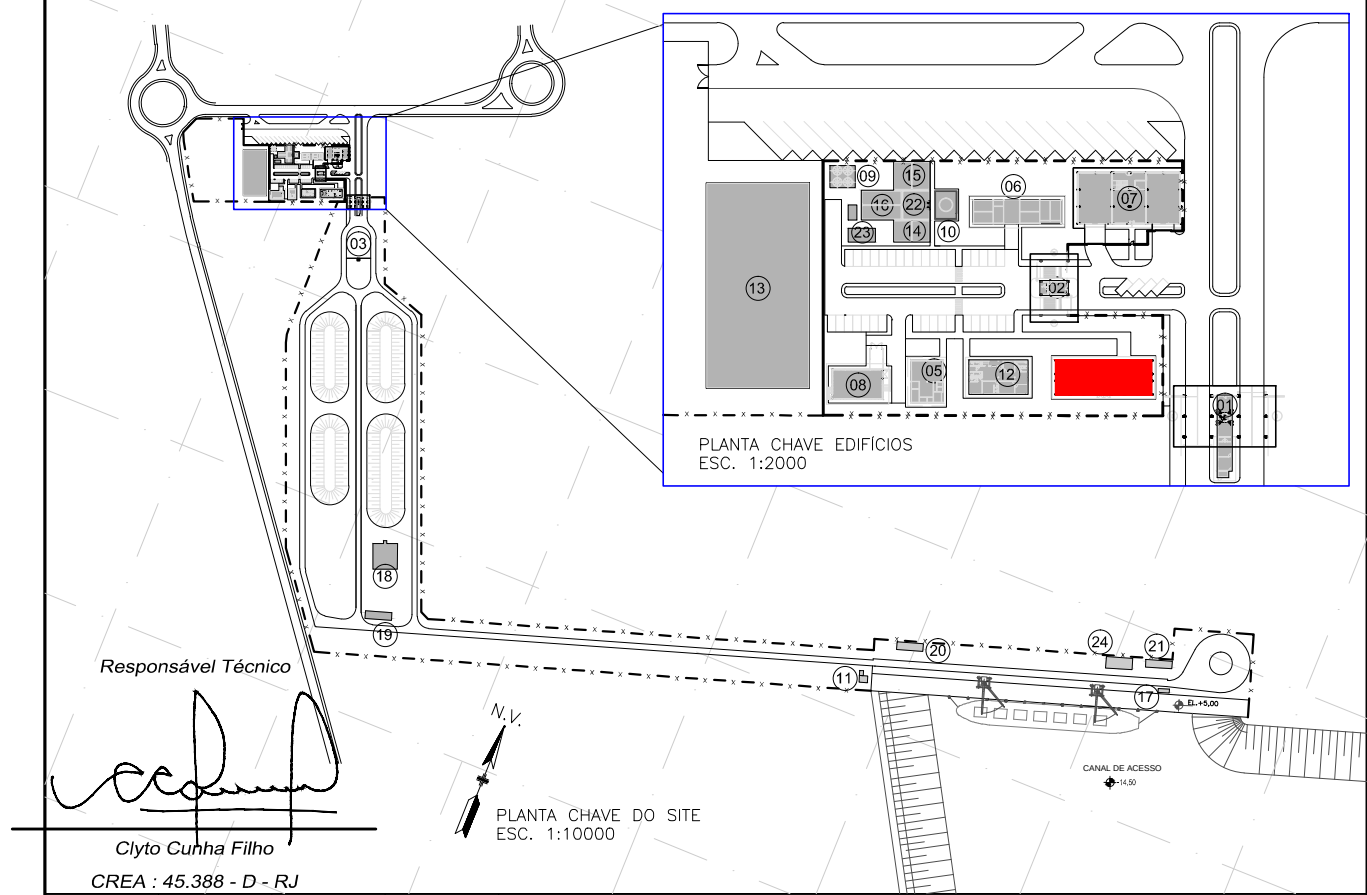

REV.	DATA	TIPO	POR	DESCRIÇÃO DAS REVISÕES
A	18/03/15	B	LMX	ALTERADA PLANTA CHAVE - PARA COMENTÁRIOS
0	30/01/15	B	LMX	EMIÇÃO INICIAL

TIPO DE EMISSÃO	(A) PRELIMINAR (B) P/COMENTÁRIOS (C) P/CONHECIMENTO	(D) P/COTAÇÃO (E) P/CONSTRUÇÃO (F) CONFORME COMPRADO	(G) CONFORME CONSTRUÍDO (H) CANCELADO (I) APROVADO	(L) LIB. P/COMPRA (M) CERTIFICADO
-----------------	---	--	--	--------------------------------------

PRUMO LABORATÓRIO DE PROJETO		AÇU OPERAÇÕES PORTUÁRIAS S/A	
engesique		PORTO DO AÇU - PROJETO EXECUTIVO	
RESPONSÁVEL		DATA	
PROJ.	LMX	30/01/15	
DES.	FBA	30/01/15	
VERIF.	ENG.RODRIGO	30/01/15	ESCALA
APROV.	ENG.CLYTO	30/01/15	INDICADA
No. PROJ.		No. PROJETA	
AÇU-3.DES-2.3100-64-EGS-008		FORMATO	
REV. A		A1	